
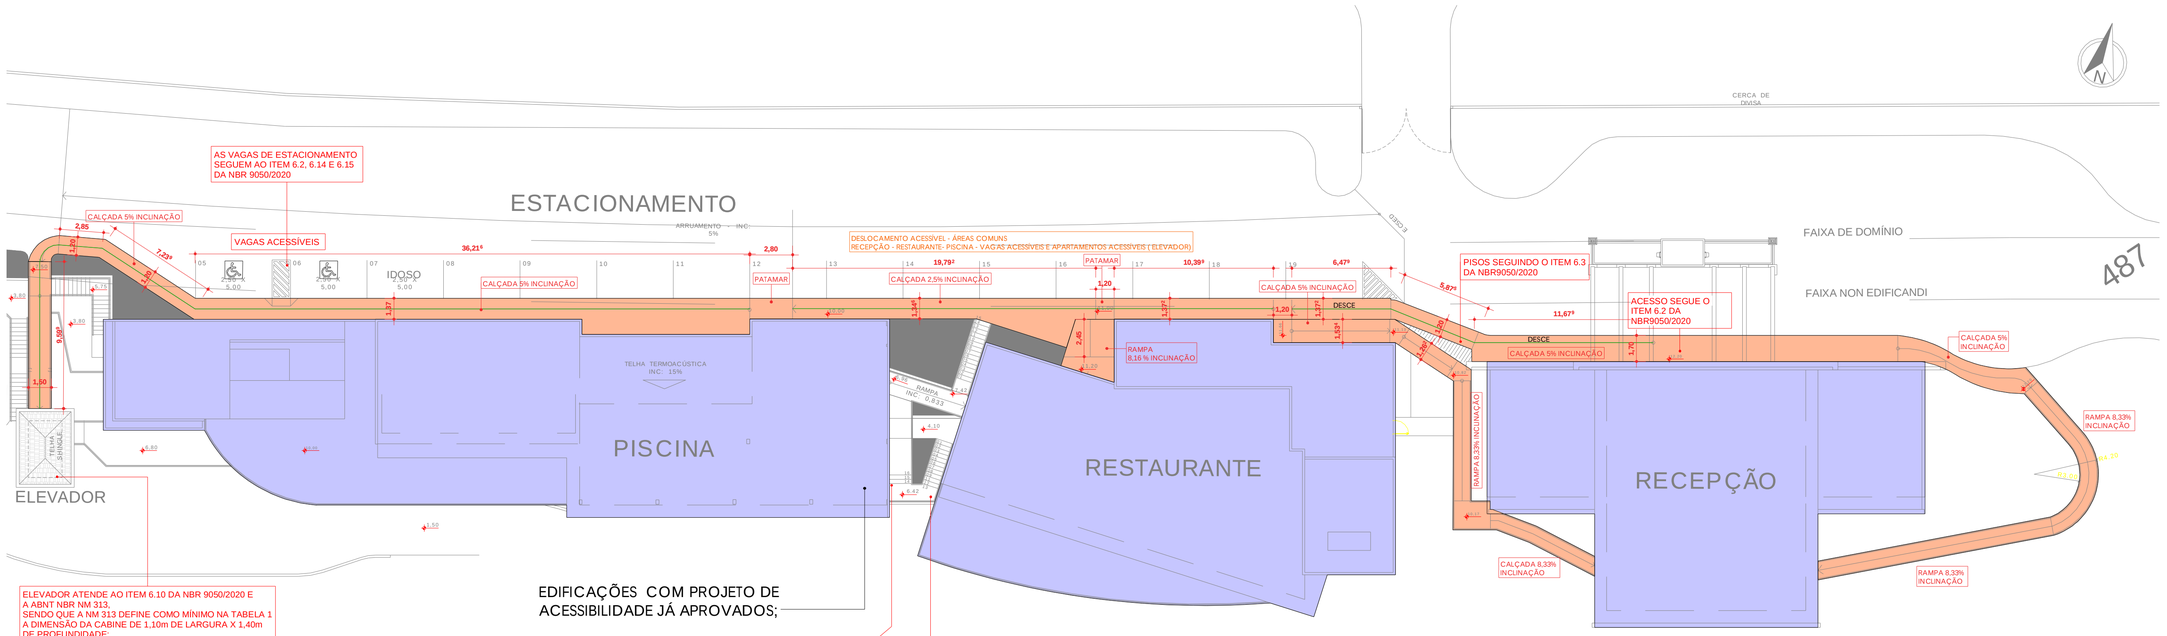



1 **IMPLANTAÇÃO ACESSIBILIDADE**

1 : 200

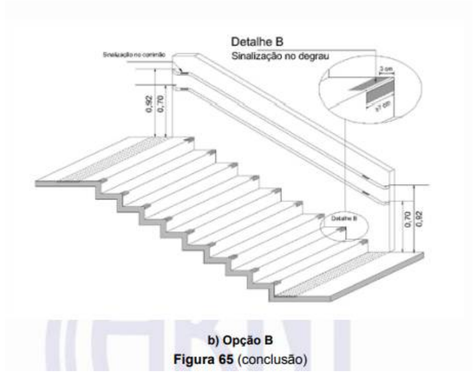


**b) Opção B**
**Figura 65** (conclusão)



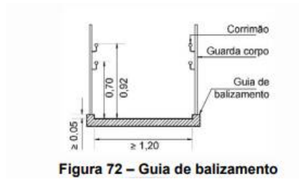



**Figura 72 – Guia de balizamento**

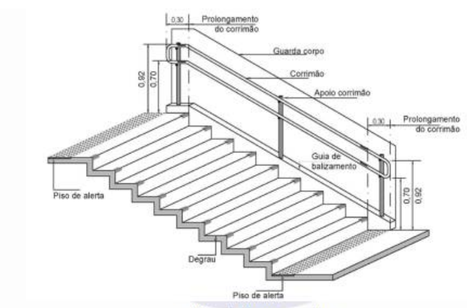


**a) Corrimão em escadas**

**FIGURA 76 - CORRIMÃO**

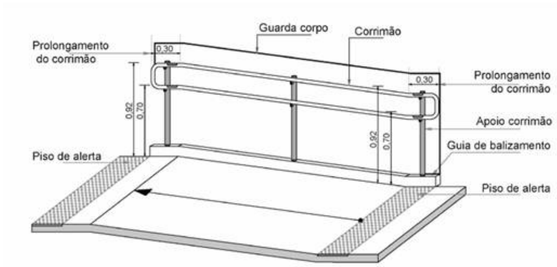


**b) Corrimão em rampas**

**Figura 76 – Corrimãos em escada e rampa**

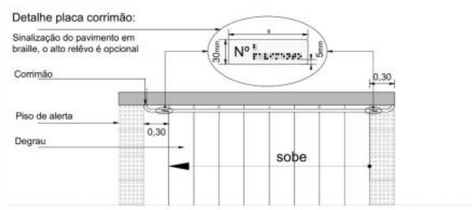



**Figura 63 – Sinalização de corrimão – Vista superior**

Dimen

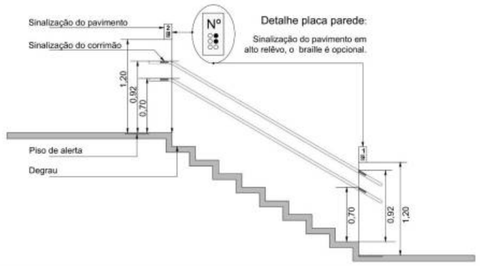



**Figura 64 – Sinalização de pavimento – Vista lateral**

| Nº | MODIFICAÇÕES / REVISÕES | RESP./PROJE | APROVADO | DATA |
|---|---|---|---|---|
| 0 | EMISSÃO INICIAL | ELIS | ELIS | 21/04/2025 |
| 1 | RETORNO | ELIS | ELIS | 22/12/2025 |
| 2 | | | | |
| 3 | | | | |

ELIS REGINA arquitetura & interiores
MICHEL HORN engenharia & interiores

# ACESSIBILIDADE

Obra: POUSADA VÔ TESTA
Área: 2.785,49
Endereço: RODOVIA LAGO AZUL
Quadra: -
Lote:

PROPRIETÁRIO: FLÁVIO CALGARO

RESPONSÁVEL TÉCNICO: **ELIS REGINA STADTLOBER** ARQ. E URB. - CAU A116328-0

Conteúdo da folha: IMPLANTAÇÃO GERAL

Projetista: Autor
Escala: INDICADA
Data e Versão: 22/12/2025 - R01
Formato: **A1** - 841x594 mm

Prancha: **AC-01**

OS DIREITOS AUTORAIS DESTE PROJETO SÃO RESERVADOS, É PROIBIDA SUA REPRODUÇÃO, MODIFICAÇÃO, ALTERAÇÃO E/OU SUA UTILIZAÇÃO INDEVIDA. LEI 5968 ART. 25.

C:\Outros computadores\Meu laptop\Projetos Michel Horn\Clientes 2024\23-POUSADA VÔ TESTA\ACESSIBILIDADE\AC01-R01 POUSADA VÔ TESTA.vrt