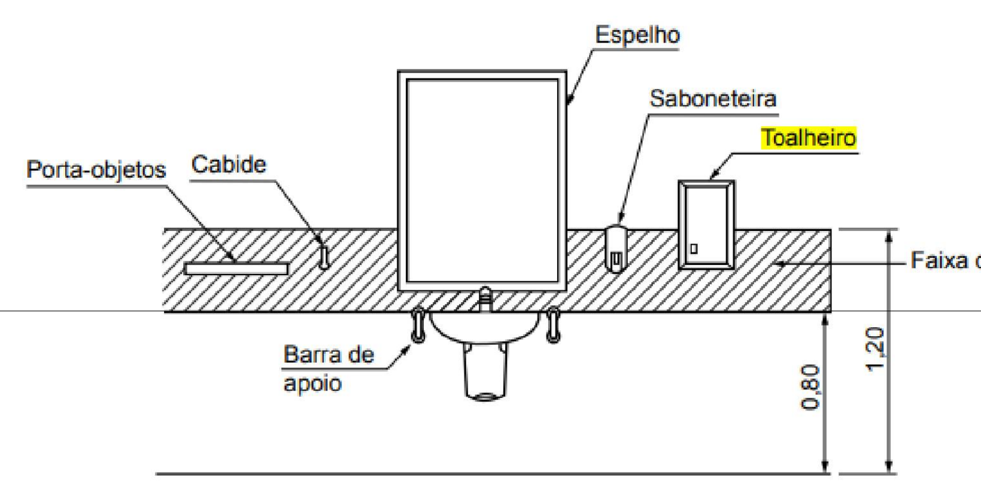
Espelho
Saboneteira
Toalheiro
Porta-objetos
Cabide
Faixa de alcance
Barra de apoio
0,80
1,20

Figura 121 – Faixa de alcance de acessórios junto ao lavatório – Vista frontal

PORTA OBJETOS, CABIDE, SABONETEIRA E TOALHEIRO DEVEM SER INSTALADOS DENTRO DA FAIXA DE ALCANCE, ENTRE 0,80 A 1,20 M

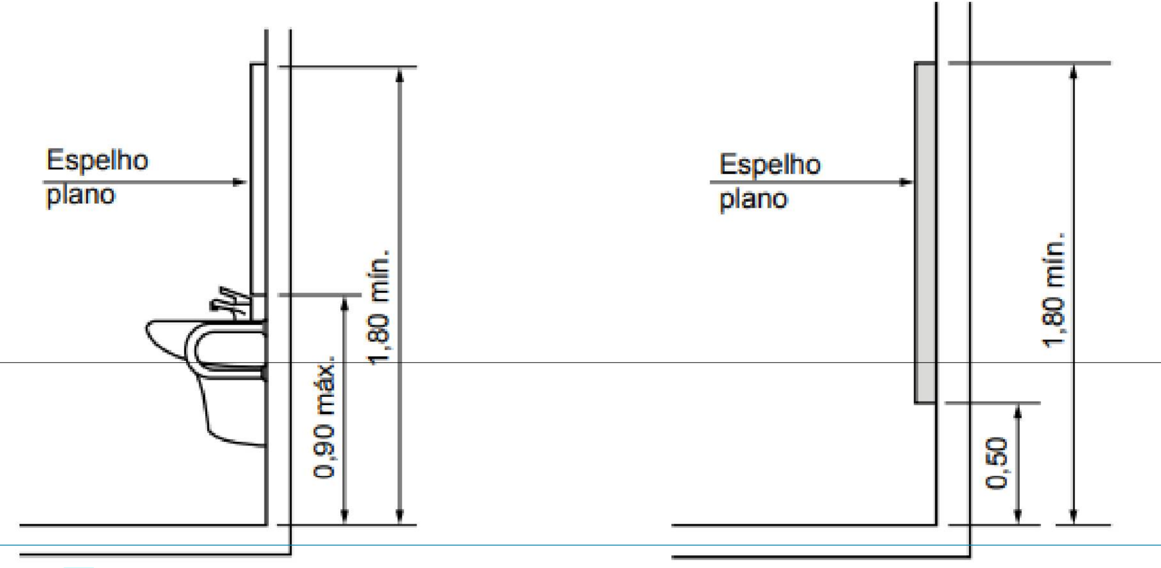
Espelho plano
0,90 máx.
1,80 mín.
Espelho plano
0,50
1,80 mín.

Figura 122 – Altura de instalação do espelho – Vista lateral

O MÉTODO DE ACIONAMENTO DA DESCARGA, TORNEIRA E TRINCO SERÁ POR ALAVANCA SENDO QUE A TORNEIRA DEVE ESTAR A NO MÁXIMO 50 CM DA PARTE FRONTAL DO LAVATÓRIO

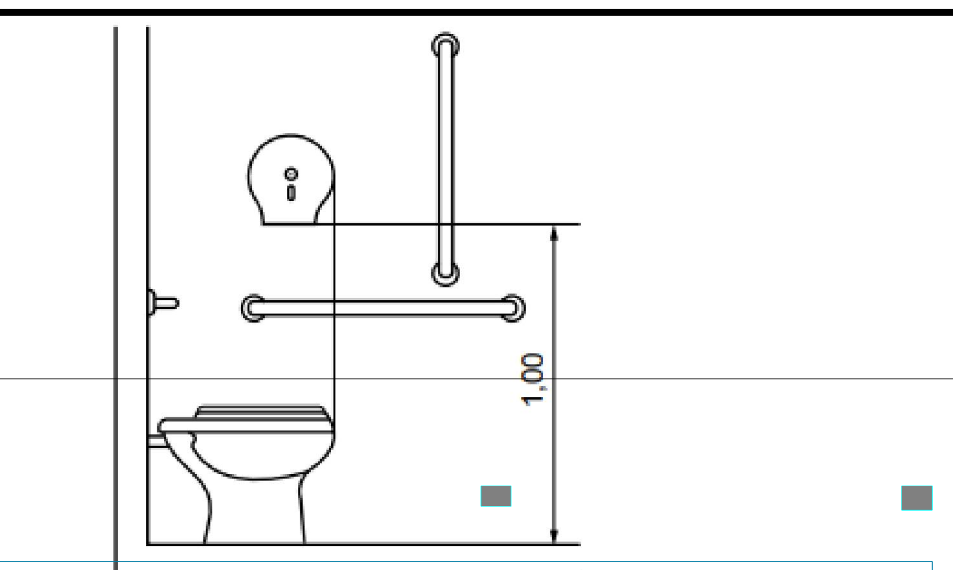

Figura 124 – Localização da papeleira de sobrepor (rolo) – Vista lateral

1,50
7,50
DESCE
14
13
12
6,97
11
10
09
08
07
06
05
04
03
02
01
5,04
PASSARELA
A:11,95 m²
GUARDA-CORPO - 1,10m
1,50
6,84
DESCE
1,50¹
ELEV.
A: 3,24 m²
PASSARELA
A: 32,95 m²
6,80
GUARDA-CORPO - 1,10m
3,28⁹
1,24⁸
ROUPARIA
A:15,50 m²
CIRCULAÇÃO
P: Conc. Estampado
PISO ANTIDERRAPANTE
A: 91,82m²
6,90
2,00
COZ/SALA
A:15,02 m²
CIRC.
A:1,94 m²
WC
A:3,75 m²
DORM.
A:9,26 m²
WC
A:4,56 m²
QUARTO
A:20,83 m²
QUARTO
A:21,03 m²
WC
A:3,97 m²
WC
A:3,97 m²
QUARTO
A:16,69 m²
QUARTO
A:16,63 m²
WC
A: 4,27 m²
APARTAMENTO ACESSÍVEL ATENDE O DECRETO 9296/2018
QUARTO (PcD)
A: 24,21m²
WC
A:4,83 m²
WC
A:4,12 m²
DORM
A:11,40 m²
COZ.
A:10,04 m²
SOBE
6,80
2,00

ESCADAS ATENDERÃO AOS ITENS 6.8 E 6.9 DA NBR 9050/2020

O ELEVADOR ATENDERÁ A ABNT NBR NM 313 E TAMBÉM A 9050/2020

ACESSOS E CIRCULAÇÕES ATENDENDO AOS ITEM 6 DA NBR9050/2020 DESTACANDO OS ITENS 6.1; 6.2 ; 6.3 E 6.4 PARA ESTE PAVIMENTO;

1 ACESSIBILIDADE - NÍVEL 7.0

1 : 75

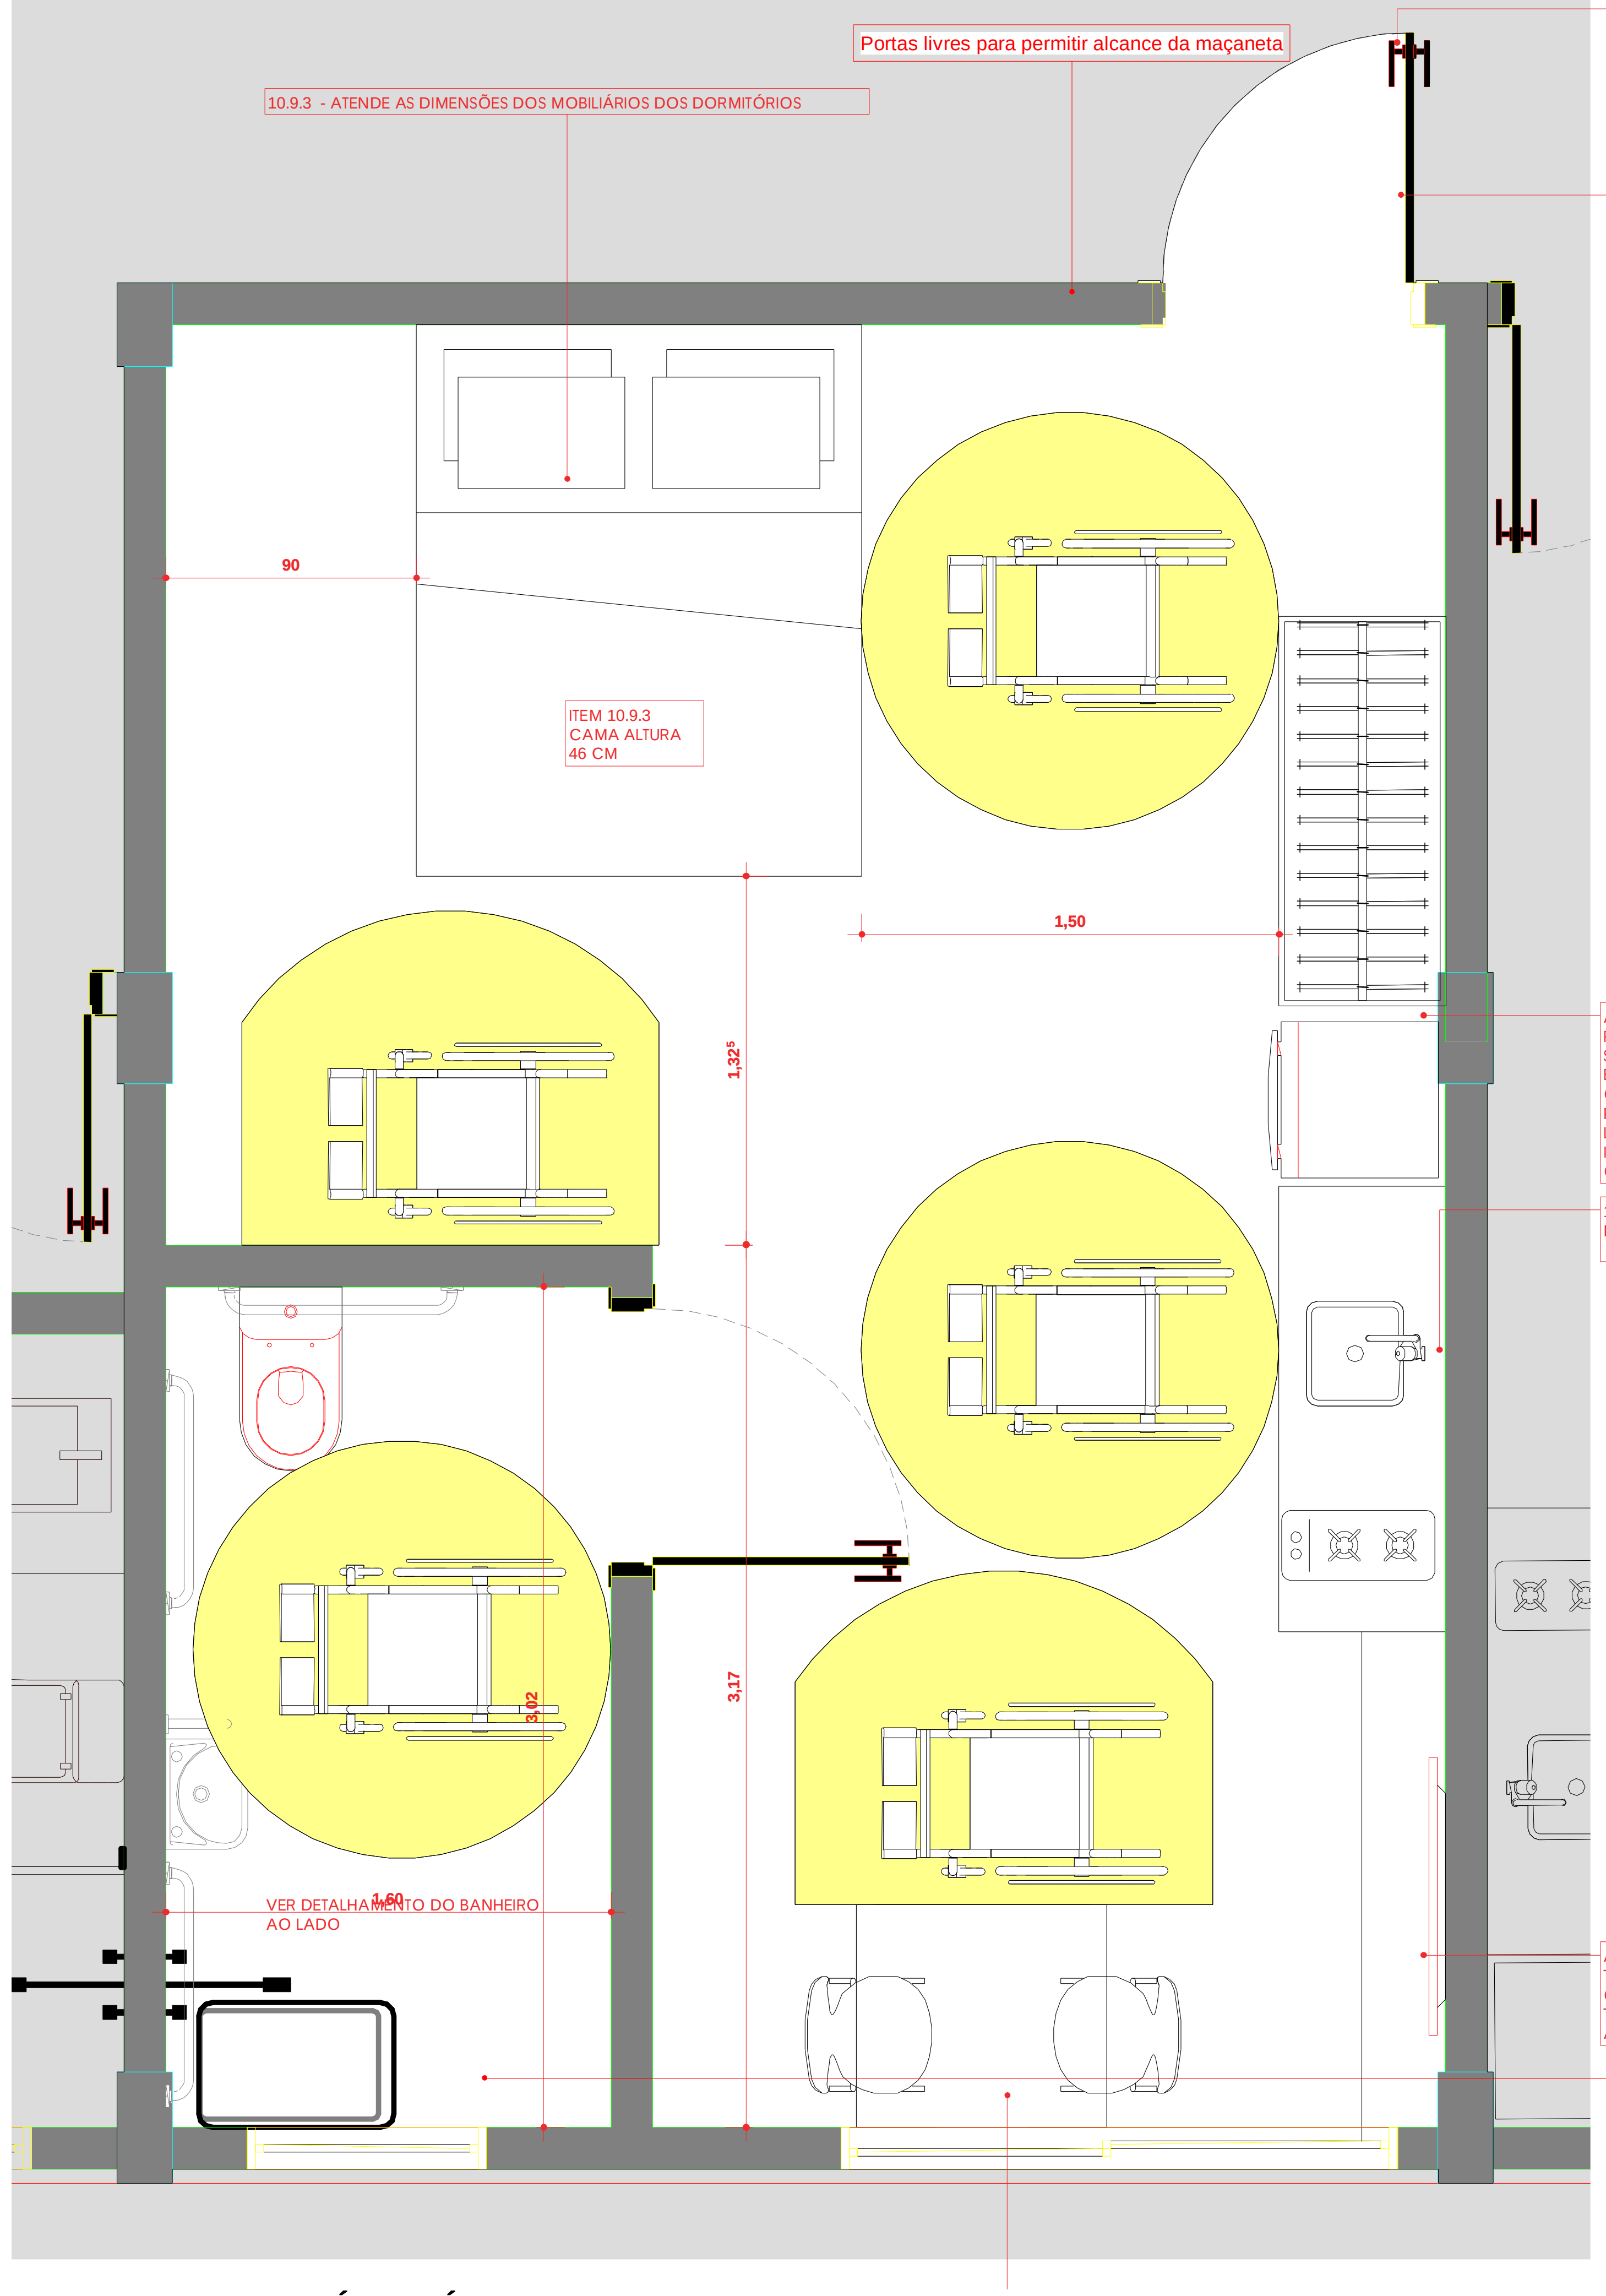
90
ITEM 10.9.3
CAMA ALTURA
46 CM
1,50
1,32⁶
3,17
3,02
VER DETALHAMENTO DO BANHEIRO AO LADO
1,60

Portas livres para permitir alcance da maçaneta

10.9.3 - ATENDE AS DIMENSÕES DOS MOBILIÁRIOS DOS DORMITÓRIOS

ANEXO I - DECRETO FED.9296/2018 : SISTEMA MAGNÉTICO DE TRANCA DAS PORTAS DOS DORMITÓRIOS QUE PERMITA AUTONOMIA AO HÓSPEDE COM DEFICIÊNCIA VISUAL, SURDO OU SURDO-CEGO, ALÉM DE INFORMAÇÕES DE RELEVO, RANHURAS OU CORTES NOS ESCANINHOS DE LEITURA E NOS CARTÕES MAGNÉTICOS;

ANEXO I - DECRETO FED.9296/2018 VÃO DE PASSAGEM LIVRE MÍNIMO DE OITENTA CENTÍMETROS PARA A PORTA DA UNIDADE E PARA A PORTA DO BANHEIRO

ANEXO I - DECRETO FED.9296/2018 - SINALIZAÇÃO DE EMERGÊNCIA, PARA OS CASOS DE INCÊNDIO OU PERIGO, SONORA E LUMINOSA INTERMITENTE(FLASH) NA COR VERMELHA;

10.9.7 - ATENDE AS DIMENSÕES DE APROXIMAÇÃO DA COZINHA

ANEXO I - DECRETO FED.9296/2018 - APARELHO DE TELEVISÃO COM DISPOSITIVO RECEPTORES DE LEGENDA OCULTA E DE ÁUDIO SECUNDÁRIO;
TELEFONE COM TIPOLOGIA AMPLIADA E COM AMPLIFICADOR DE SINAL;

APARTAMENTO ACESSÍVEL ATENDE AO DECRETO FEDERAL 9296/2018
ANEXO I - CORRESPONDENTE A 5% DAS UNIDADES DE HOSPEDAGEM;

2 APTO ACESSÍVEL - NÍVEL 7.0

1 : 25

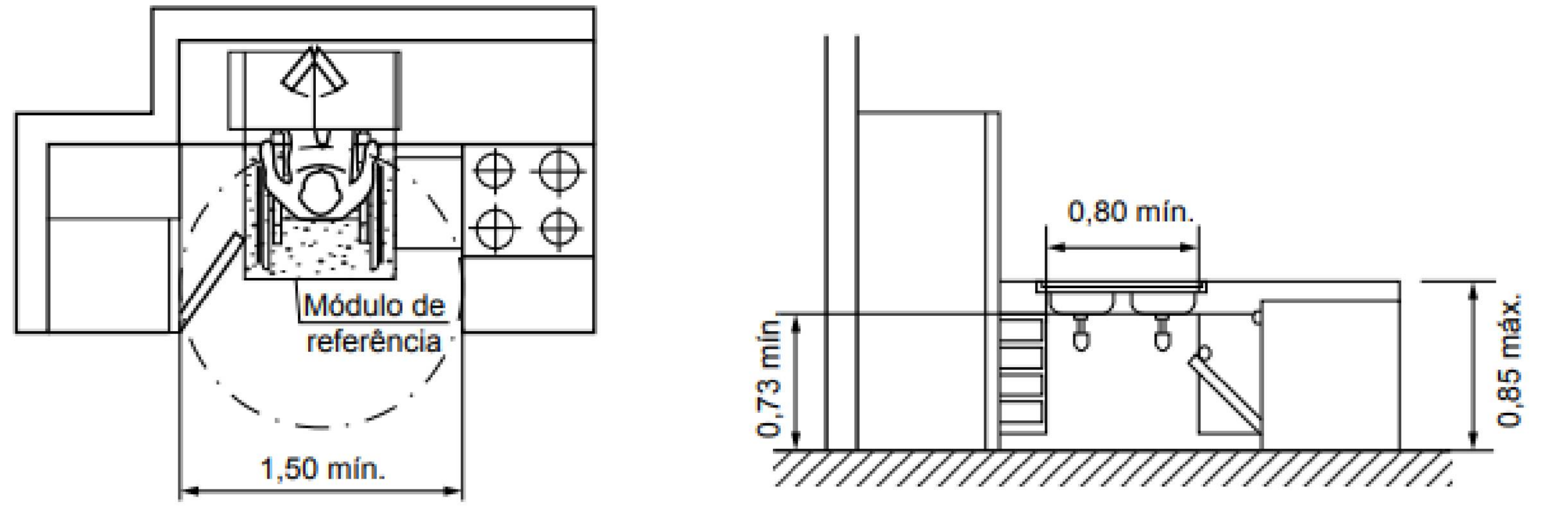
Módulo de referência
1,50 mín.
0,80 mín.
0,73 mín
0,85 máx.

a) Vista superior

b) Vista frontal

Figura 147 – Cozinha – Área de aproximação e medidas para uso

NOTA:

SANITÁRIOS ATENDEM AOS ITENS

7.3 LOCALIZAÇÃO
7.4 QUANTIFICAÇÃO E CARACTERÍSTICAS
7.5 DIMENSÕES
7.6 BARRAS DE APOIO
7.7 ALTURA, POSIÇÃO E DIMENSÃO DAS BARRAS E SANITÁRIO
7.8 ALTURA, POSIÇÃO E DIMENSÃO DAS BARRAS DE APOIO DO LAVATÓRIO
7.12.3 BARRAS DE APOIO EM BOX PARA CHUVEIROS;

COMO SEGUE NOS DETALHAMENTOS INDIVIDUAIS

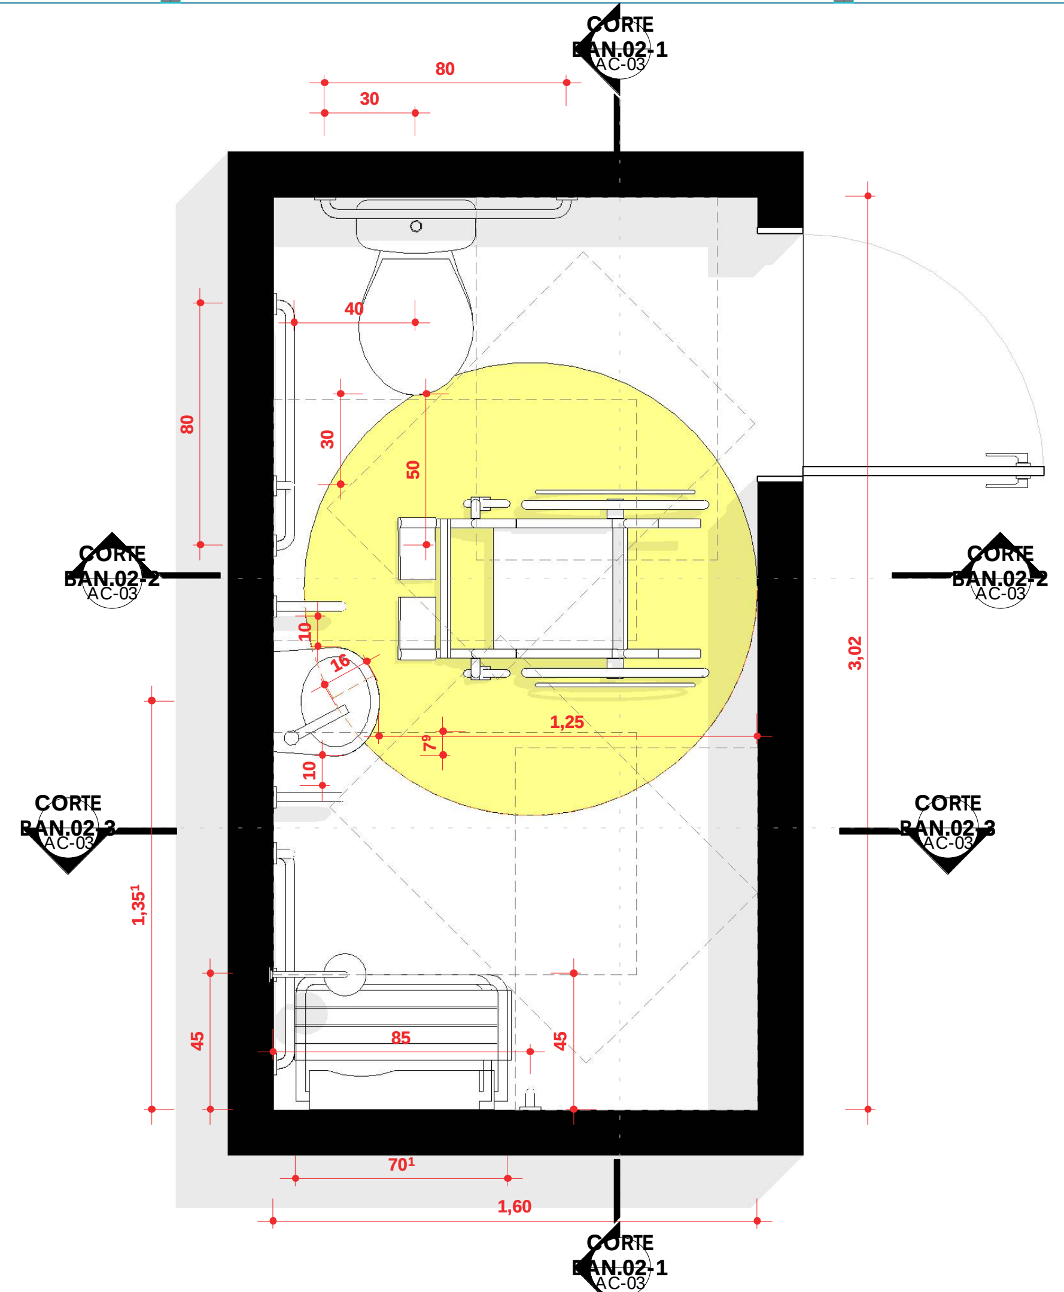
CORTE BAN.02-1 AC-03
80
30
40
30
50
80
10
10
1,25
3,02
CORTE BAN.02-2 AC-03
CORTE BAN.02-3 AC-03
1,35¹
45
85
45
70¹
1,60
CORTE BAN.02-1 AC-03

3 TÉRREO ANTEPROJETO

1 : 25

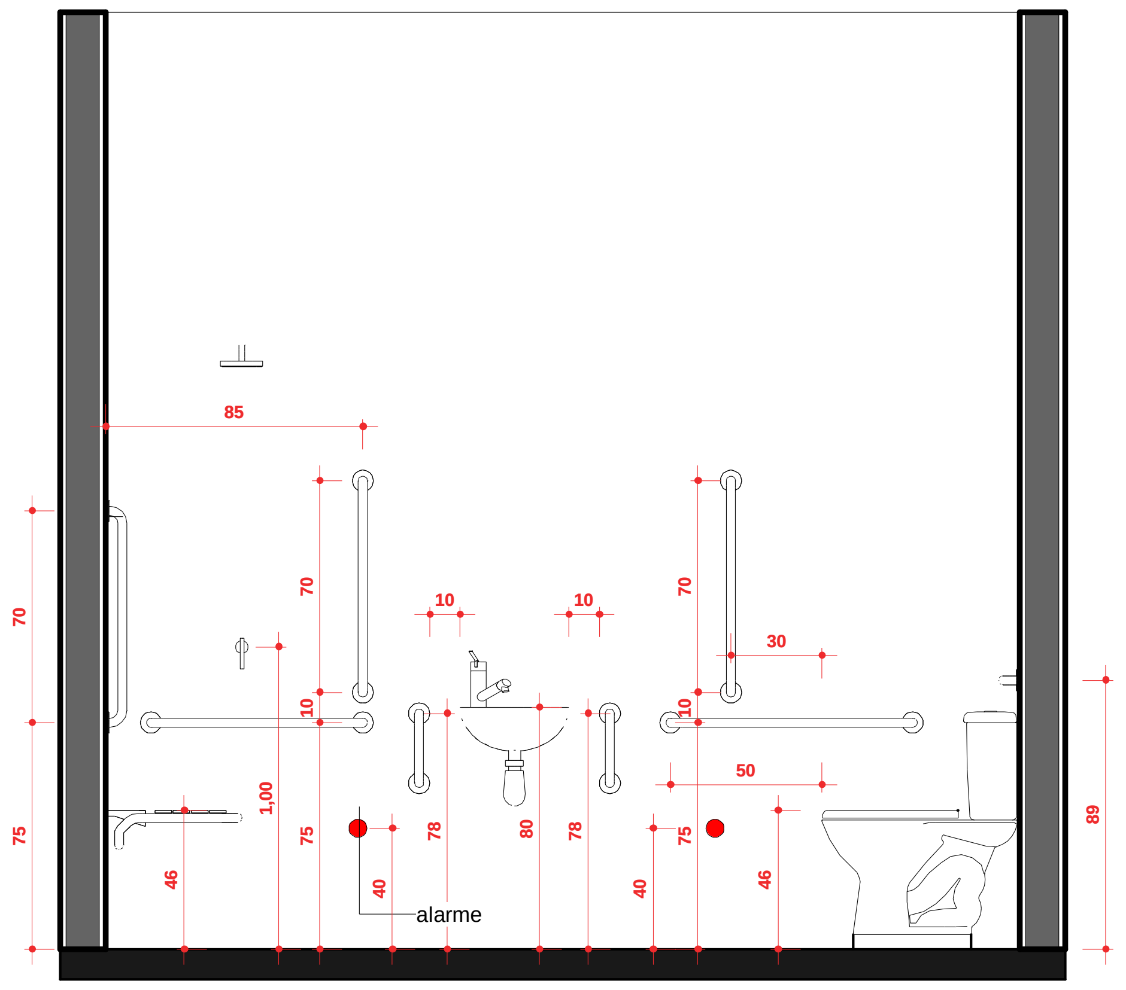
85
70
10
10
70
30
10
50
70
75
46
1,00
75
40
78
80
78
40
75
46
89
alarme

4 CORTE BAN.02-1

1 : 25

TODOS OS DEMAIS APARTAMENTO ATENDEM AO ANEXO II DO DECRETO 9296/2018:

- VÃO DE PASSAGEM LIVRE MÍNIMO DE OITENTA CENTÍMETROS PARA PORTA DA UNIDADE E PARA A PORTA DO BANHEIRO
- BARRA DE APOIO NO BOX DO CHUVEIRO
- CHUVEIRO EQUIPADO COM BARRA DESLIZANTE, DESVIADOR PARA DUCHA MANUAL E CONTROLE DE FLUXO(DUCHA/CHUVEIRO) NA DUCHA MANUAL (CHUVEIRINHO), O QUAL DEVERÁ ESTAR SEMPRE POSICIONADO NA ALTURA MAIS BAIXA QUANDO DA CHEGADA DO HÓSPEDE);
-SISTEMA MAGNÉTICO DE TRANCA DAS PORTAS DOS DORMITÓRIOS QUE PERMITA AUTONOMIA AO HÓSPEDE COM DEFICIÊNCIA VISUAL, SURDO OU SURDO-CEGO ALÉM DE INFORMAÇÕES EM RELEVO, RANHURAS, OU CORTES NOS ESCANINHOS DE LEITURA E NOS CARTÕES MAGNÉTICOS;
- SINALIZAÇÃO DE EMERGÊNCIA, PARA OS CASOS DE INCÊNDIO OU PERIGO, SONORA E LUMINOSA INTERMITENTE(FLASH) NA COR VERMELHA;
-APARELHO DE TELEVISÃO COM DISPOSITIVOS RECEPTORES DE LEGENDA OCULTA E DE ÁUDIO SECUNDÁRIO;
-TELEFONE COM TIPOLOGIA AMPLIADA E COM AMPLIFICADOR DE SINAL, QUANDO O DORMITÓRIO DISPONIBILIZAR ESSE TIPO DE APARELHO;

ANEXO III DO DECRETO 9296/2018 - QUANDO SOLICITADO:

-CADEIRA DE RODAS
-CADEIRAS ADAPTADAS PARA BANHO
-MATERIAIS DE HIGIENE IDENTIFICADO EM BRAILE E EMBALAGENS EM FORMATOS DIFERENTES;
-MATERIAIS IMPRESSOS DISPONÍVEIS EM FORMATO DIGITAL, BRAILE, FONTE AMPLIADA EM CONTRASTE, A EXEMPLO DE FORMULÁRIOS IMPRESSOS, INFORMAÇÕES SOBRE FACILIDADES E SERVIÇOS OFERECIDOS DENTRE OUTROS, FEITOS SOB DEMANDA;
-CARDÁPIO EM BRAILE E FONTE AMPLIADA COM CONTRASTE;
-RELÓGIO DESPERTADOR/ALARME VIBRATÓRIO;
-DISPOSITIVOS MÓVEIS COM CHAMADA EM VÍDEO E MENSAGEM DISPONIBILIZADOS NAS ÁREAS COMUNS DO ESTABELECIMENTO OU APLICATIVO DE COMUNICAÇÃO CRIADO NOS TERMOS ESTABELECIDOS NO TÍTULO IV DA RESOLUÇÃO Nº 667, DE 30 DE MAIO DE 2016, DA ANATEL, QUE APROVA O REGULAMENTO GERAL DE ACESSIBILIDADE EM SERVIÇOS DE TELECOMUNICAÇÕES DE INTERESSE COLETIVO.

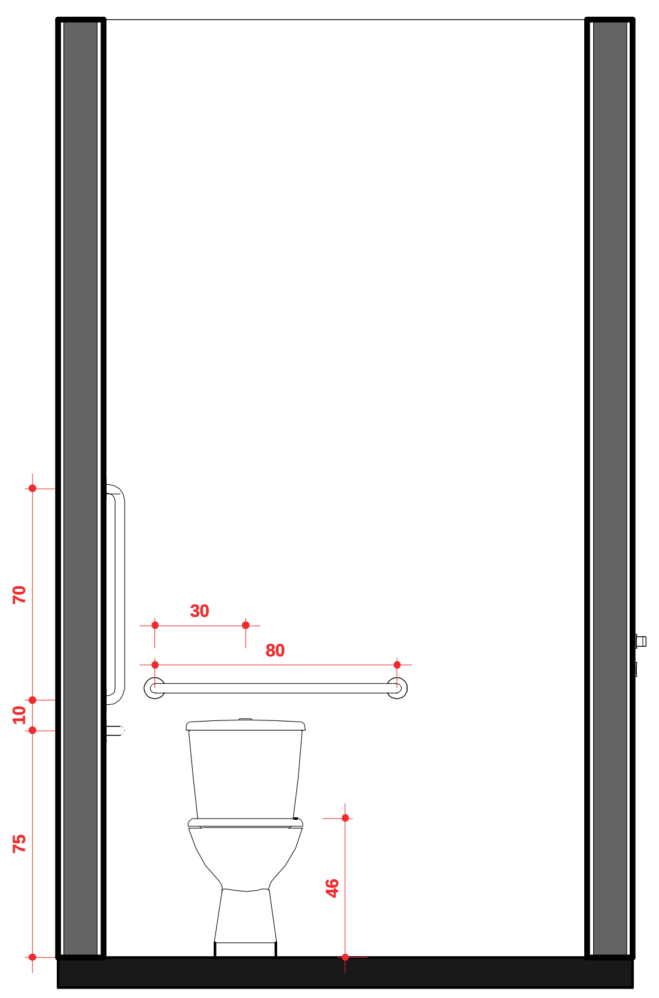
70
30
80
10
75
46
70
10
75

5 CORTE BAN.02-2

1 : 25

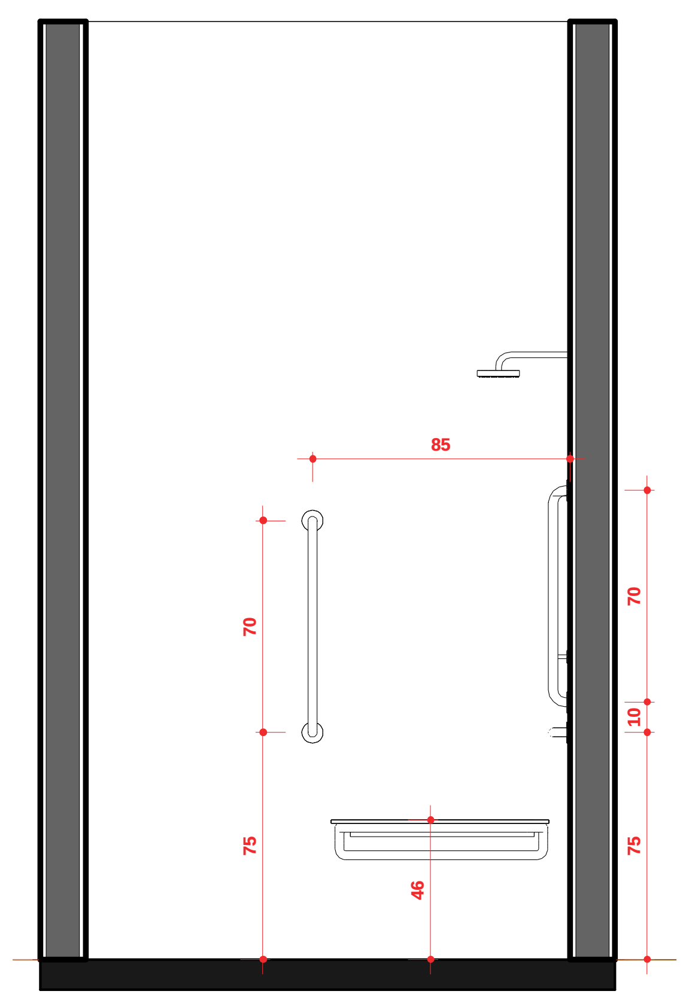
85
70
75
46
70
10
75

6 CORTE BAN.02-3

1 : 25

Nº	MODIFICAÇÕES / REVISÕES	RESP./PROJE	APROVADO	DATA
0	EMISSÃO INICIAL	ELIS	ELIS	21/04/2025
1	RETORNO	ELIS	ELIS	22/12/2025
2				
3				

ELIS REGINA
arquitetura & interiores

MICHEL HORN
engenharia & interiores

ACESSIBILIDADE

Obra:
POUSADA VÔ TESTA

Área:
2.785,49

Endereço:
RODOVIA LAGO AZUL

Quadra:
-

Lote:

PROPRIETÁRIO: FLÁVIO CALGARO

RESPONSÁVEL TÉCNICO: **ELIS REGINA STADTLOBER** ARQ. E URB. - CAU A116328-0

Conteúdo da folha:
IMPLANTAÇÃO NÍVEL 7.0
DETALHAMENTO BANHEIRO ACESSÍVEL

Projetista: Autor
Escala: INDICADA
Data e Versão: 22/12/2025 - R01
Formato: **A1** - 841x594 mm

Prancha:
AC-03

G:\Outros computadores\Meu laptop\Projetos Michel Horn\Clientes 2024\21-POUSADA VÔ TESTA\ACESSIBILIDADE\AC01-R01 POUSADA VÔ TESTA.rvt

OS DIREITOS AUTORAIS DESTE PROJETO SÃO RESERVADOS, É PROIBIDA SUA REPRODUÇÃO, MODIFICAÇÃO, ALTERAÇÃO E/OU SUA UTILIZAÇÃO INDEVIDA. LEI 5968 ART. 25.