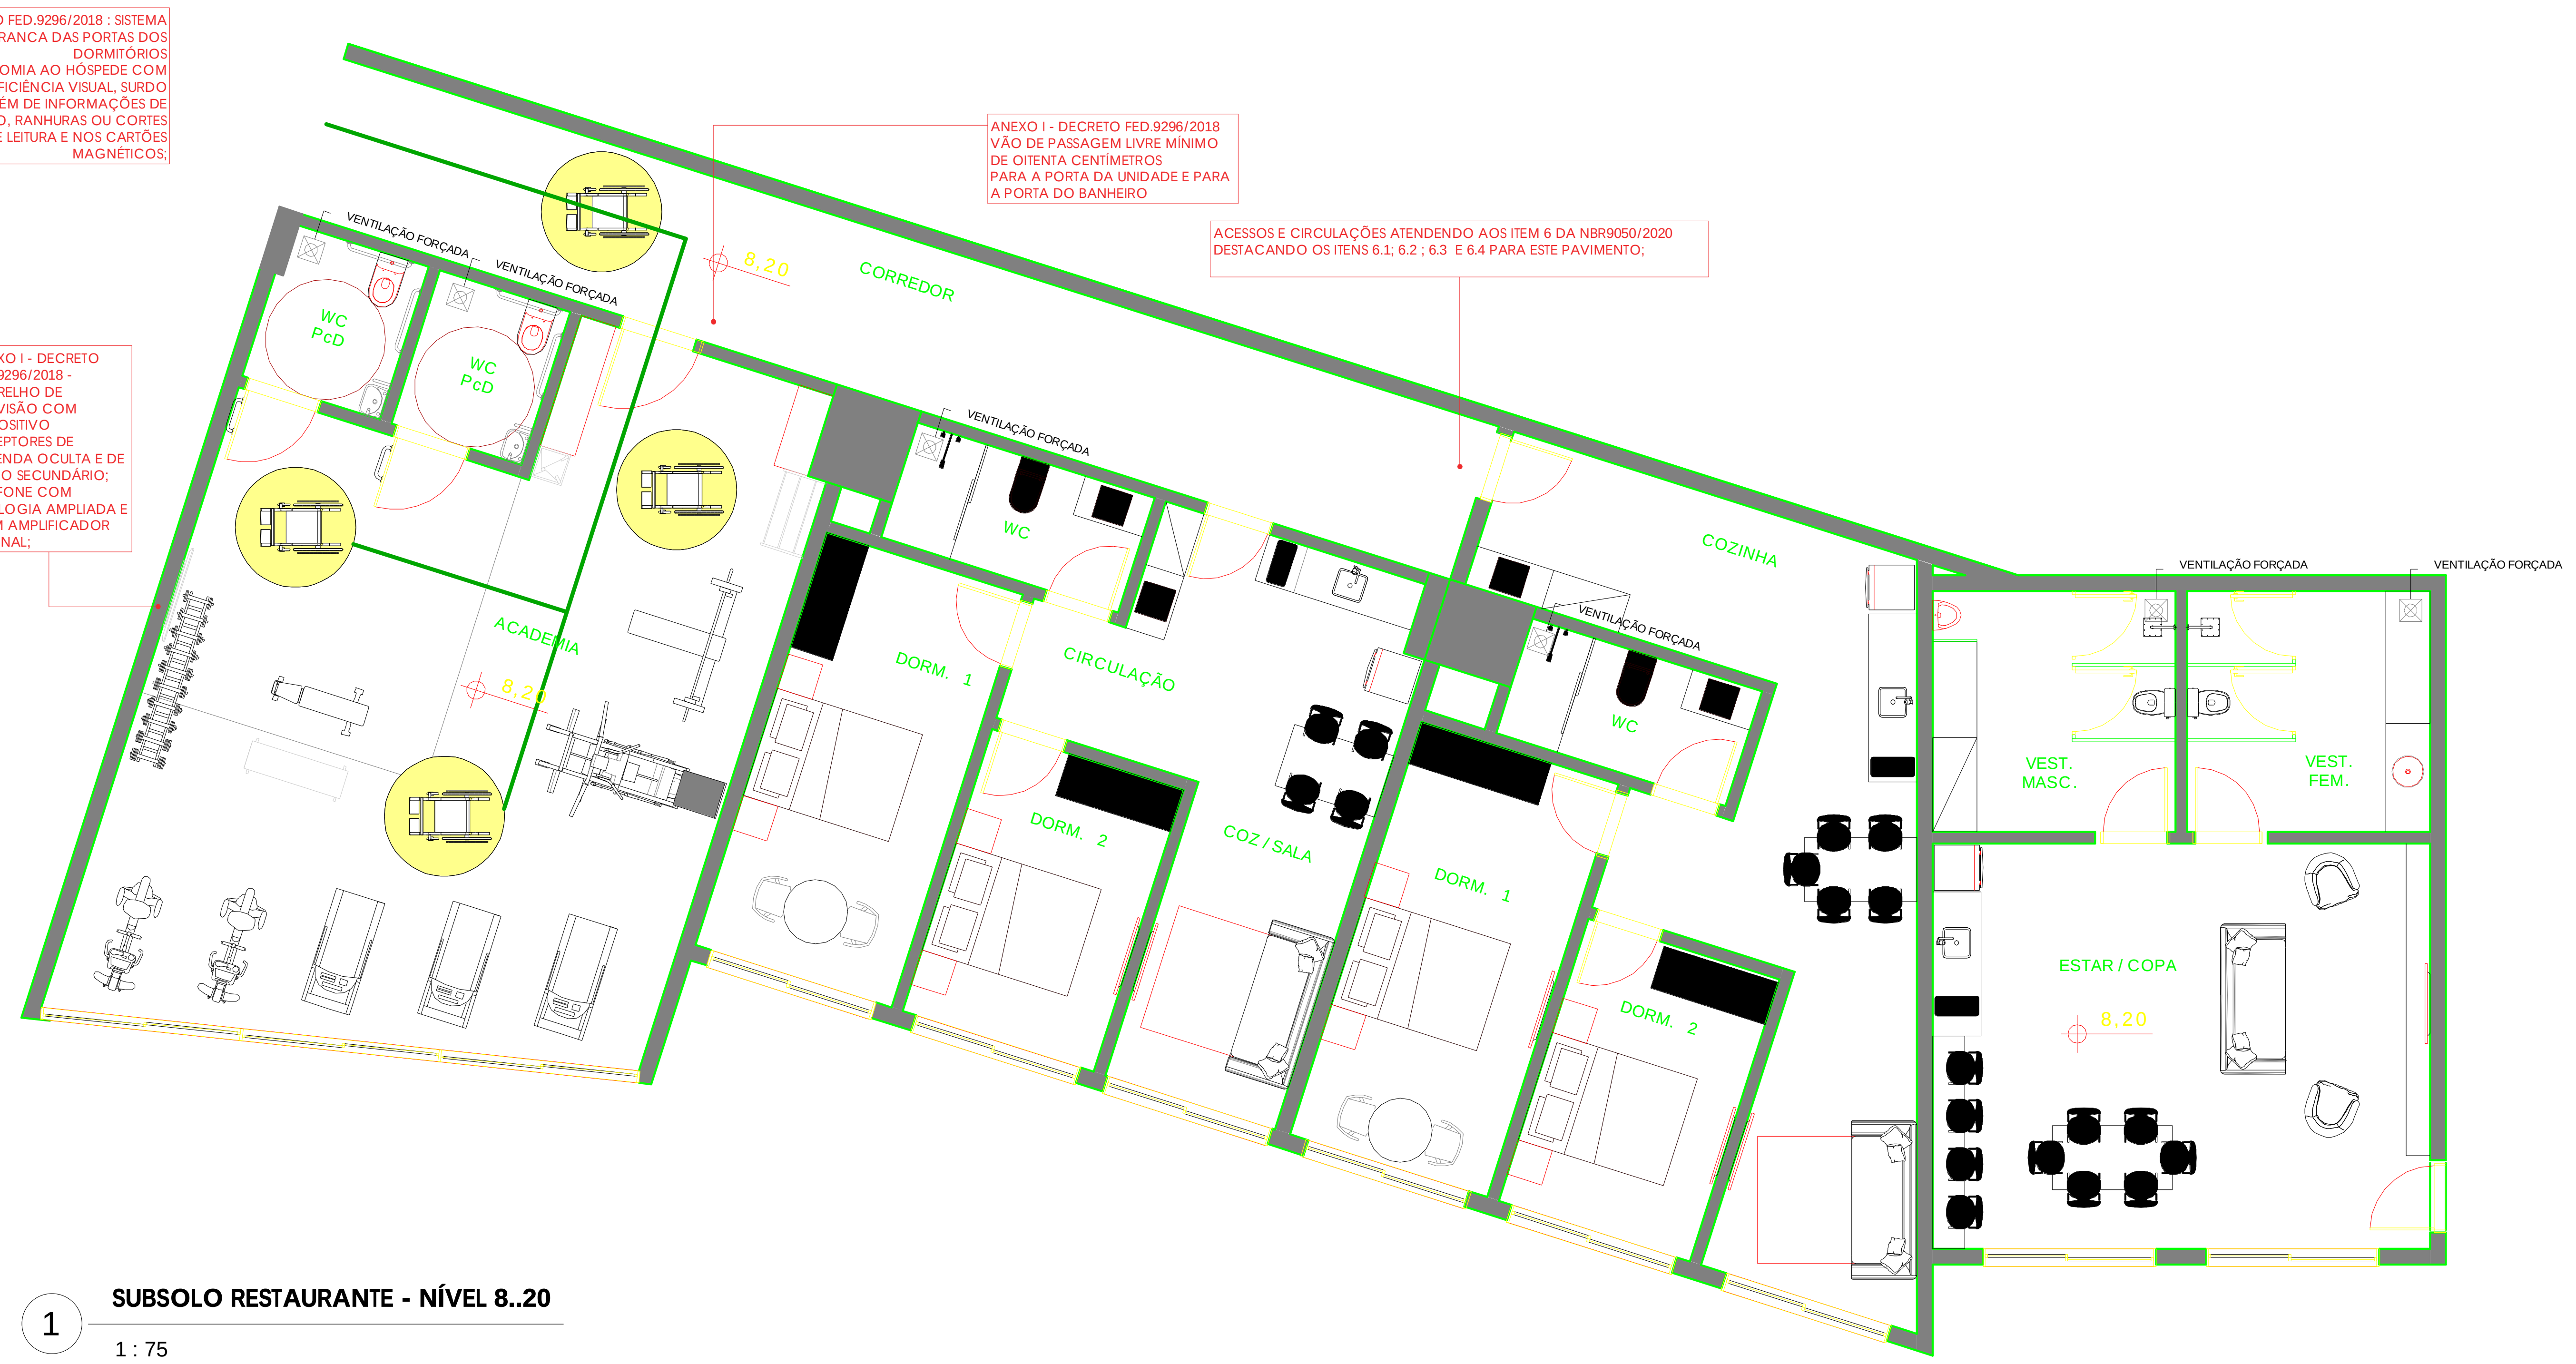

ANEXO I - DECRETO FED.9296/2018 : SISTEMA MAGNÉTICO DE TRANCA DAS PORTAS DOS DORMITÓRIOS QUE PERMITA AUTONOMIA AO HÓSPEDE COM DEFICIÊNCIA VISUAL, SURDO OU SURDO-CEGO, ALÉM DE INFORMAÇÕES DE RELEVO, RANHURAS OU CORTES NOS ESCANINHOS DE LEITURA E NOS CARTÕES MAGNÉTICOS;

ANEXO I - DECRETO FED.9296/2018 VÃO DE PASSAGEM LIVRE MÍNIMO DE OITENTA CENTÍMETROS PARA A PORTA DA UNIDADE E PARA A PORTA DO BANHEIRO

ACESSOS E CIRCULAÇÕES ATENDENDO AOS ITEM 6 DA NBR9050/2020 DESTACANDO OS ITENS 6.1; 6.2 ; 6.3 E 6.4 PARA ESTE PAVIMENTO;

ANEXO I - DECRETO FED.9296/2018 - APARELHO DE TELEVISÃO COM DISPOSITIVO RECEPTORES DE LEGENDA OCULTA E DE ÁUDIO SECUNDÁRIO; TELEFONE COM TIPOLOGIA AMPLIADA E COM AMPLIFICADOR DE SINAL;

NOTA:

SANITÁRIOS ATENDEM AOS ITENS

7.3 LOCALIZAÇÃO
7.4 QUANTIFICAÇÃO E CARACTERÍSTICAS
7.5 DIMENSÕES
7.6 BARRAS DE APOIO
7.7 ALTURA, POSIÇÃO E DIMENSÃO DAS BARRAS E SANITÁRIO
7.8 ALTURA, POSIÇÃO E DIMENSÃO DAS BARRAS DE APOIO DO LAVATÓRIO
7.12.3 BARRAS DE APOIO EM BOX PARA CHUVEIROS;

COMO SEGUE NOS DETALHAMENTOS INDIVIDUAIS

1 **SUBSOLO RESTAURANTE - NÍVEL 8..20**

1 : 75

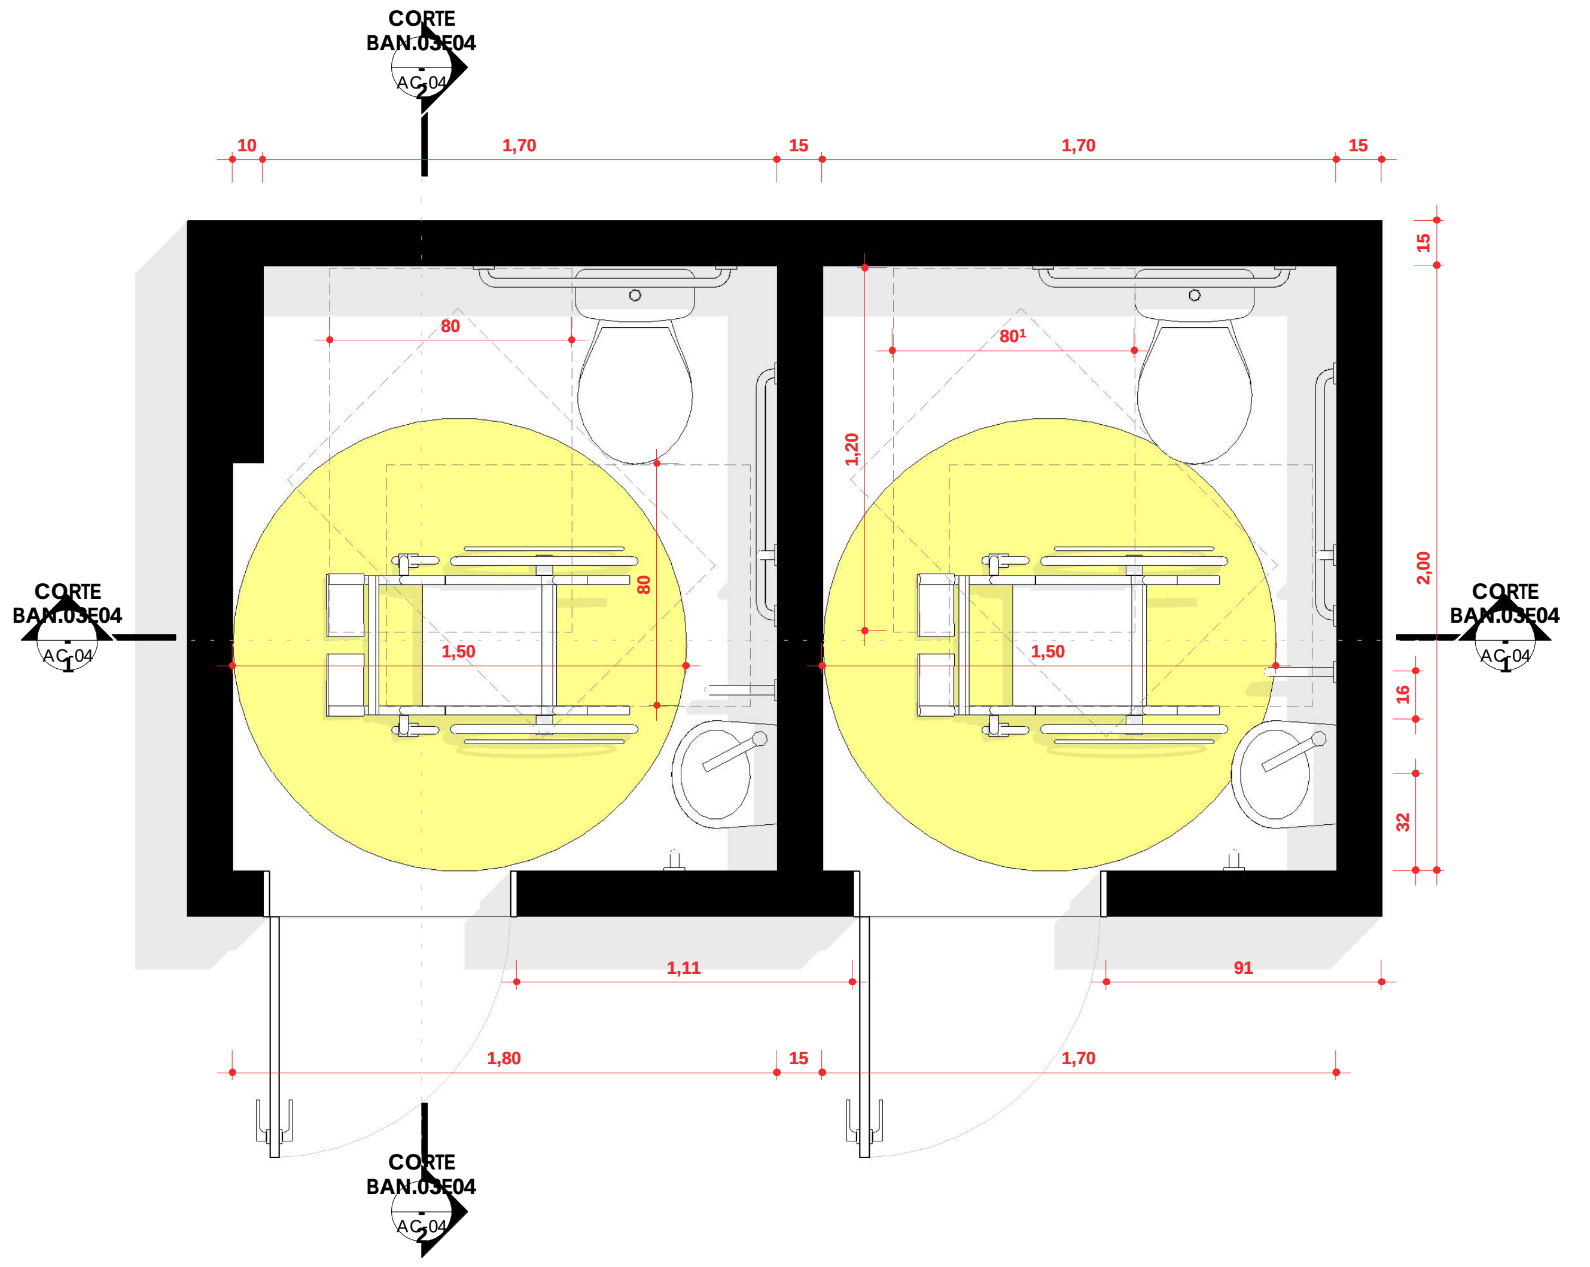
CORTE BAN.03E04 - 2 AC-04
10
1,70
15
1,70
15
80
80¹
1,20
80
1,50
1,50
2,00
16
32
CORTE BAN.03E04 - 1 AC-04
CORTE BAN.03E04 - 1 AC-04
1,11
91
1,80
15
1,70
CORTE BAN.03E04 - 2 AC-04

2 **TÉRREO ANTEPROJETO**

1 : 25

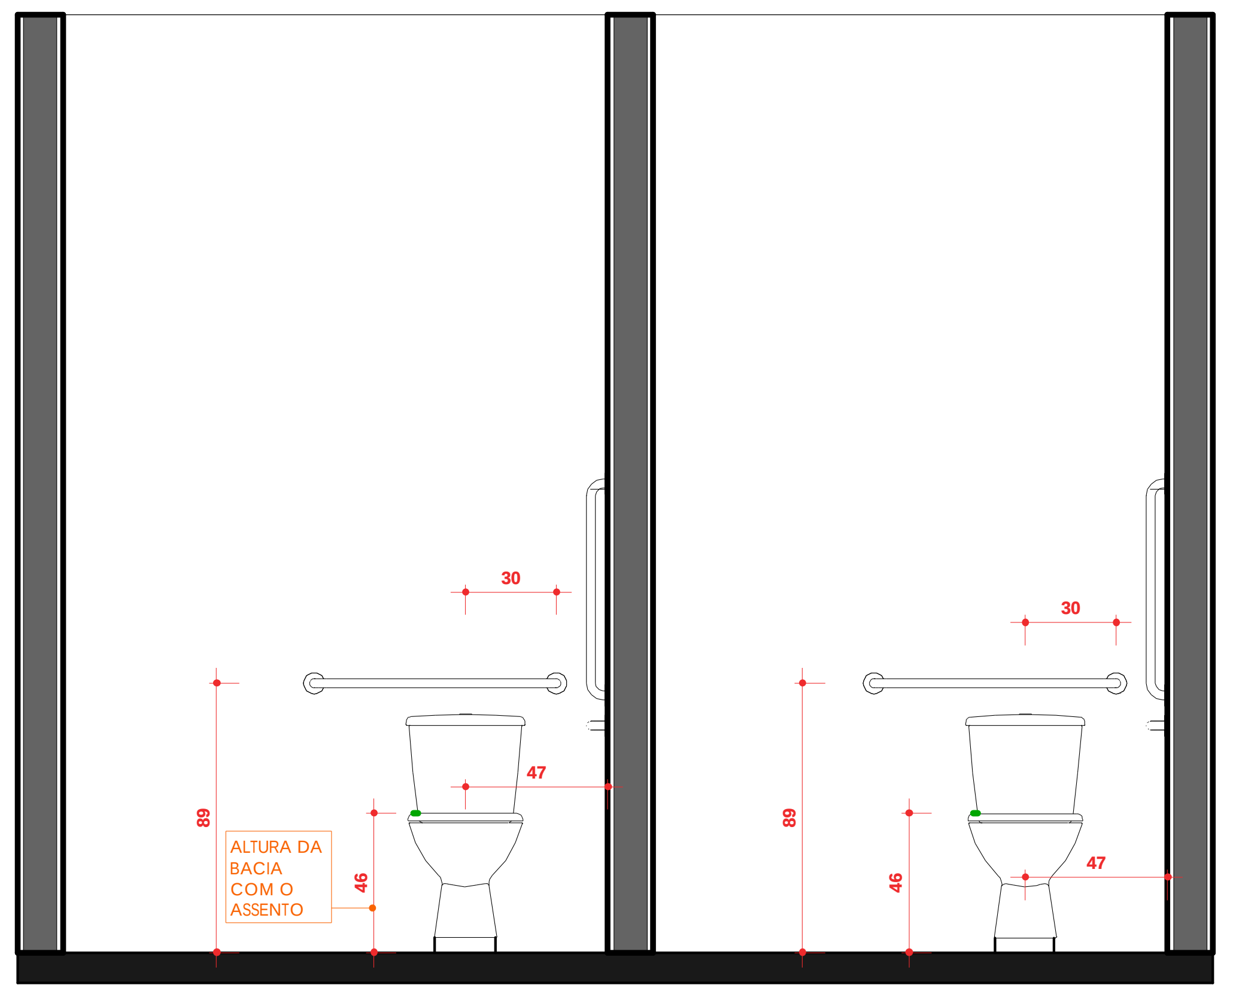

4 **CORTE BAN.03E04 - 1**

1 : 25

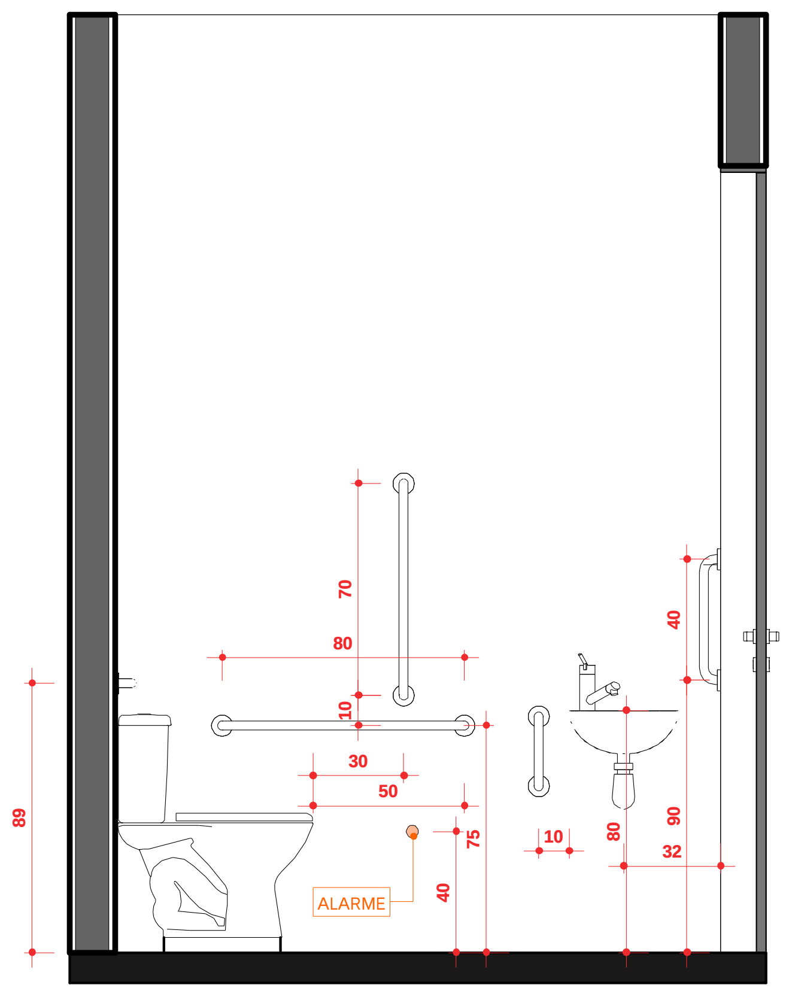

3 **CORTE BAN.03E04 - 2**

1 : 25

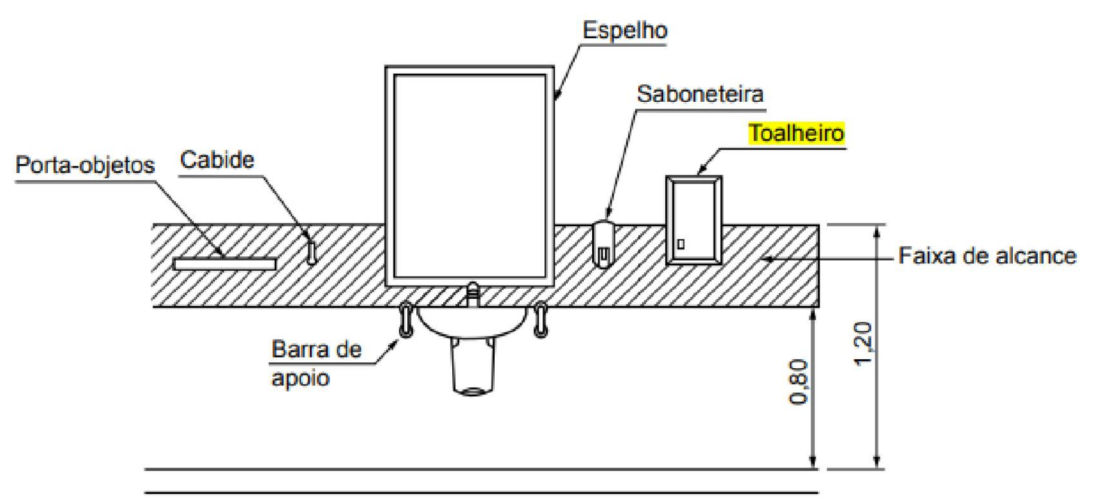

Figura 121 – Faixa de alcance de acessórios junto ao lavatório – Vista frontal

PORTA OBJETOS, CABIDE, SABONETEIRA E TOALHEIRO DEVEM SER INSTALADOS DENTRO DA FAIXA DE ALCANCE, ENTRE 0,80 A 1,20 M

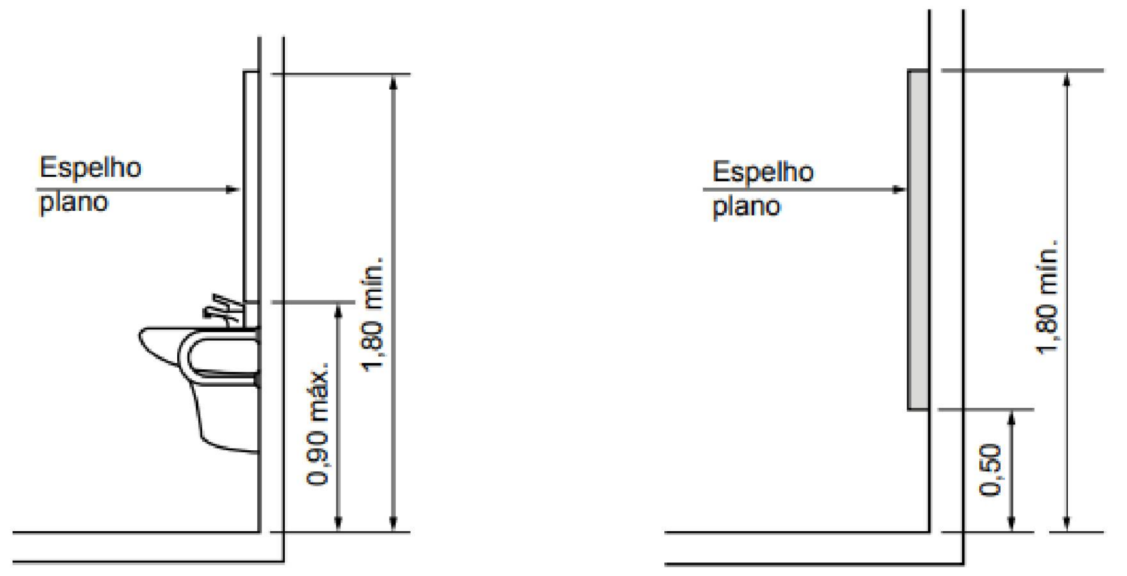

Figura 122 – Altura de instalação do espelho – Vista lateral

O MÉTODO DE ACIONAMENTO DA DESCARGA, TORNEIRA E TRINCO SERÁ POR ALAVANCA SENDO QUE A TORNEIRA DEVE ESTAR A NO MÁXIMO 50 CM DA PARTE FRONTAL DO LAVATÓRIO

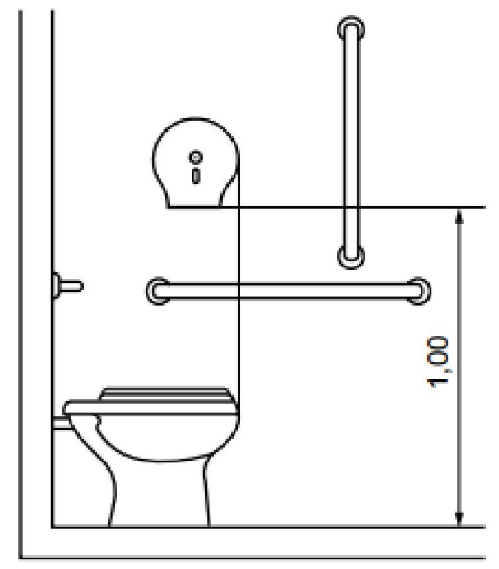

Figura 124 – Localização da papeleira de sobrepor (rolo) – Vista lateral

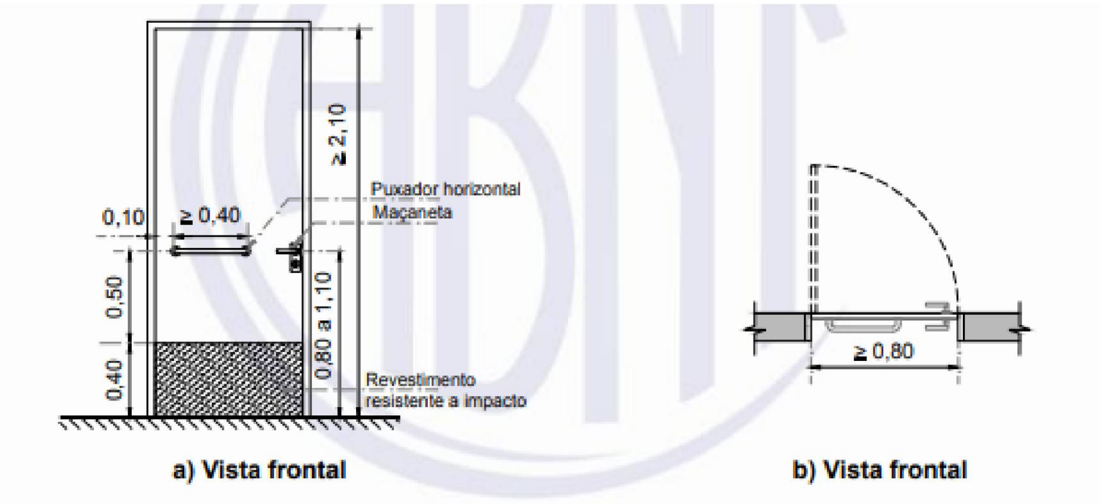

a) Vista frontal

b) Vista frontal

Figura 86 – Porta de sanitários e vestiários

Nº	MODIFICAÇÕES / REVISÕES	RESP./PROJE	APROVADO	DATA
0	EMISSÃO INICIAL	ELIS	ELIS	21/04/2025
1	RETORNO	ELIS	ELIS	22/12/2025
2				
3				

ELIS REGINA
arquitetura & interiores

MICHEL HORN
engenharia & interiores

ACESSIBILIDADE

Obra:
POUSADA VÔ TESTA

Área:
2.785,49

Endereço:
RODOVIA LAGO AZUL

Quadra:
-

Lote:

PROPRIETÁRIO: FLÁVIO CALGARO

RESPONSÁVEL TÉCNICO: **ELIS REGINA STADTLOBER** ARQ. E URB. - CAU A116328-0

Conteúdo da folha:
IMPLANTAÇÃO NÍVEL 8.2
DETALHAMENTO BANHEIRO ACESSÍVEL

Projetista: Autor
Escala: INDICADA
Data e Versão: 22/12/2025 - R01
Formato: **A1** - 841x594 mm

Prancha:
AC-04

G:\Outros computadores\Meu laptop\Projetos Michel Horn\Clientes 2024\21-POUSADA VÔ TESTA\ACESSIBILIDADE\AC01-R01 POUSADA VÔ TESTA.rvt

OS DIREITOS AUTORAIS DESTE PROJETO SÃO RESERVADOS, É PROIBIDA SUA REPRODUÇÃO, MODIFICAÇÃO, ALTERAÇÃO E/OU SUA UTILIZAÇÃO INDEVIDA. LEI 5968 ART. 25.