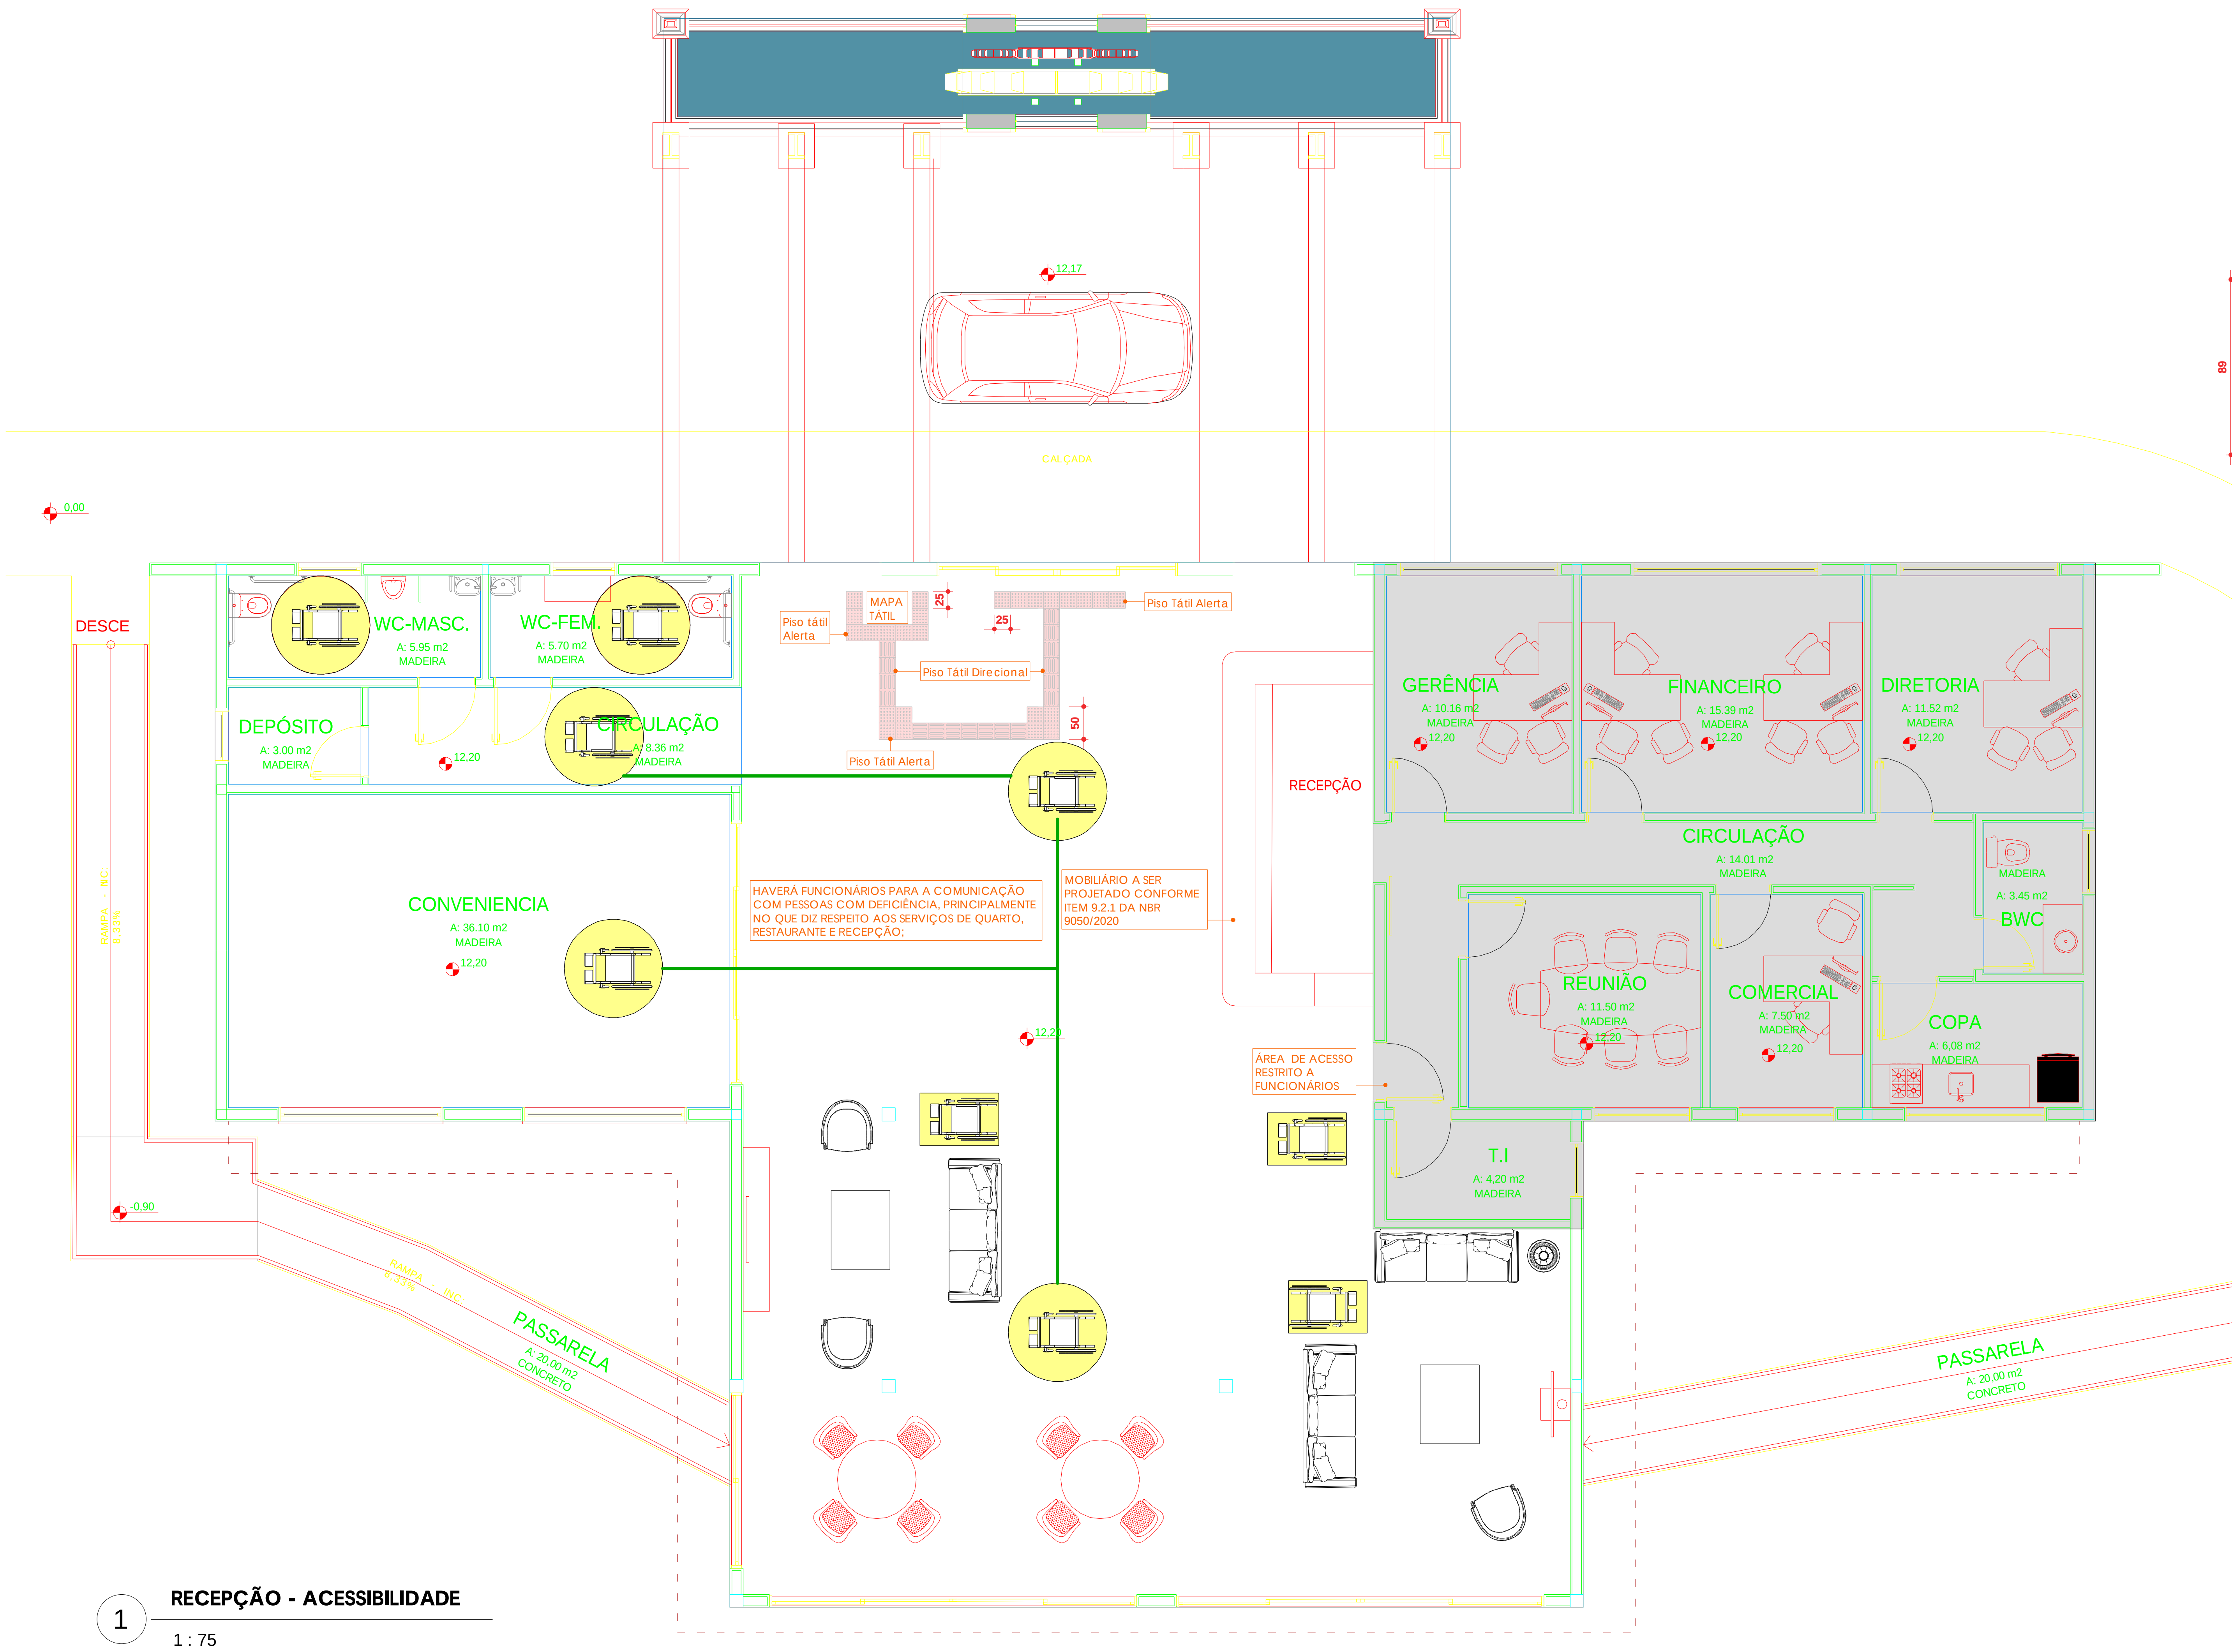

1 **RECEPÇÃO - ACESSIBILIDADE**

1 : 75

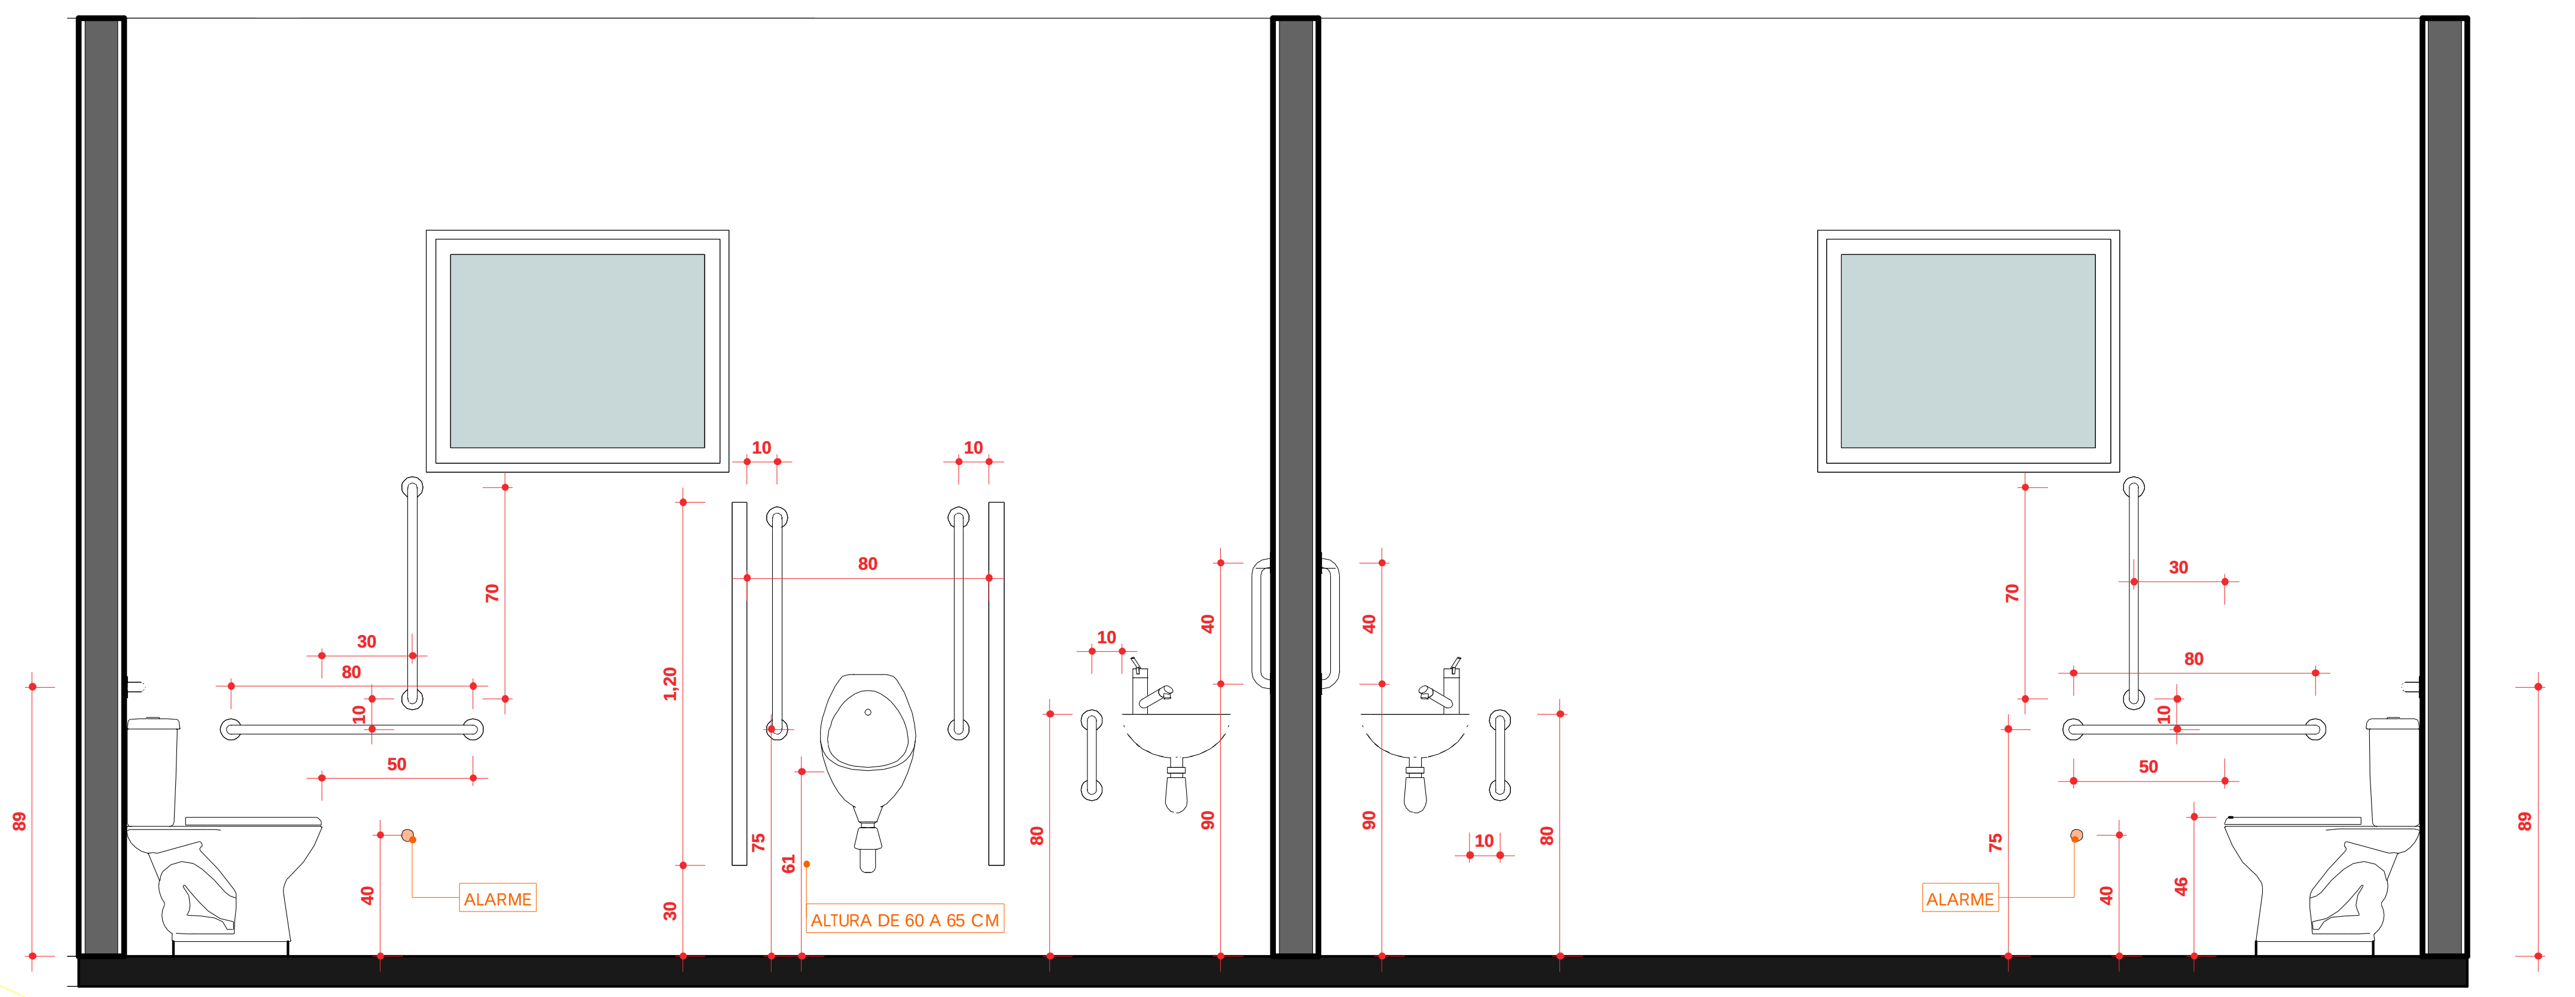

3 **CORTE BAN.05E06 -2**

1 : 25

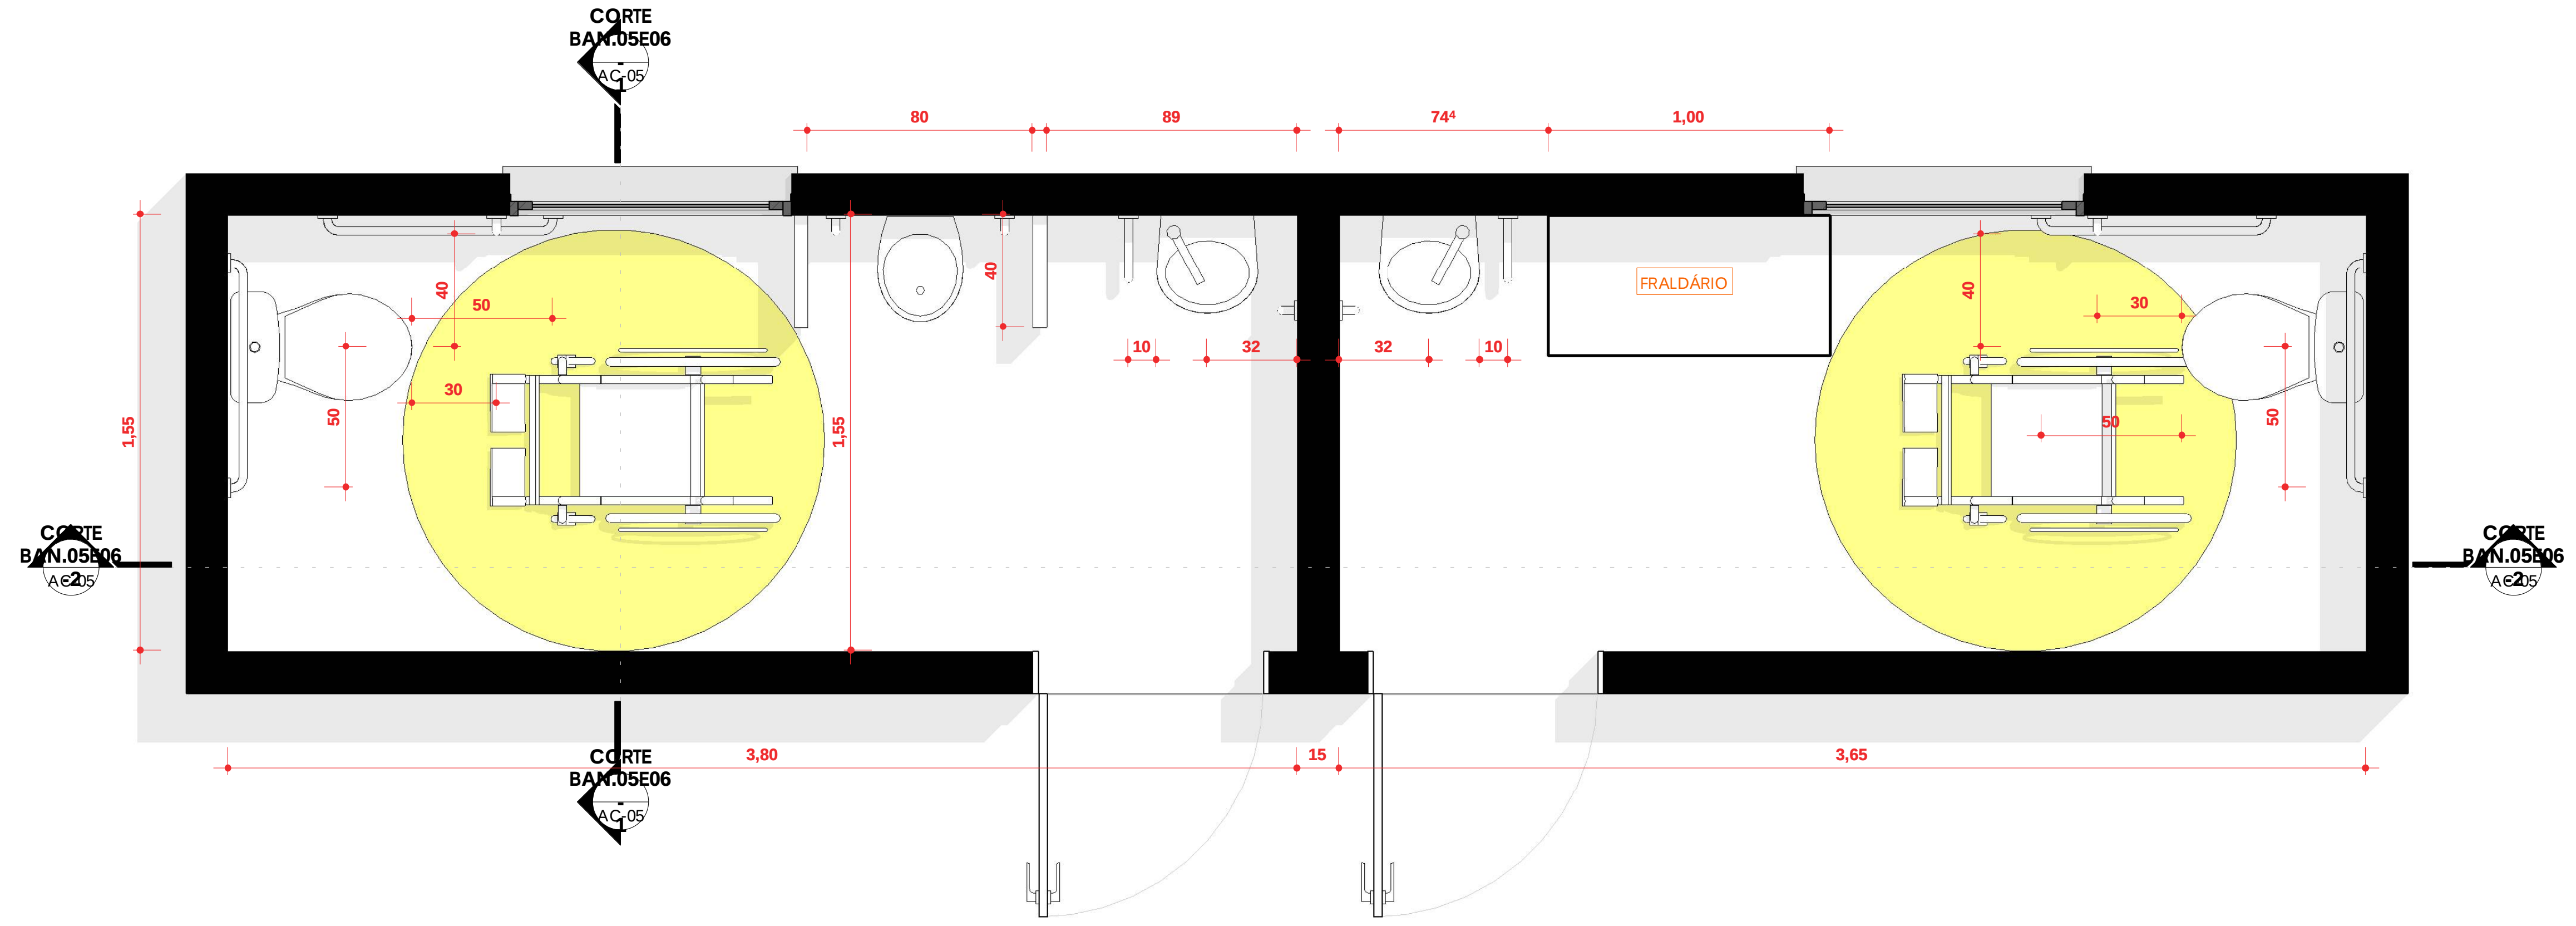

2 **TÉRREO ANTEPROJETO**

1 : 25

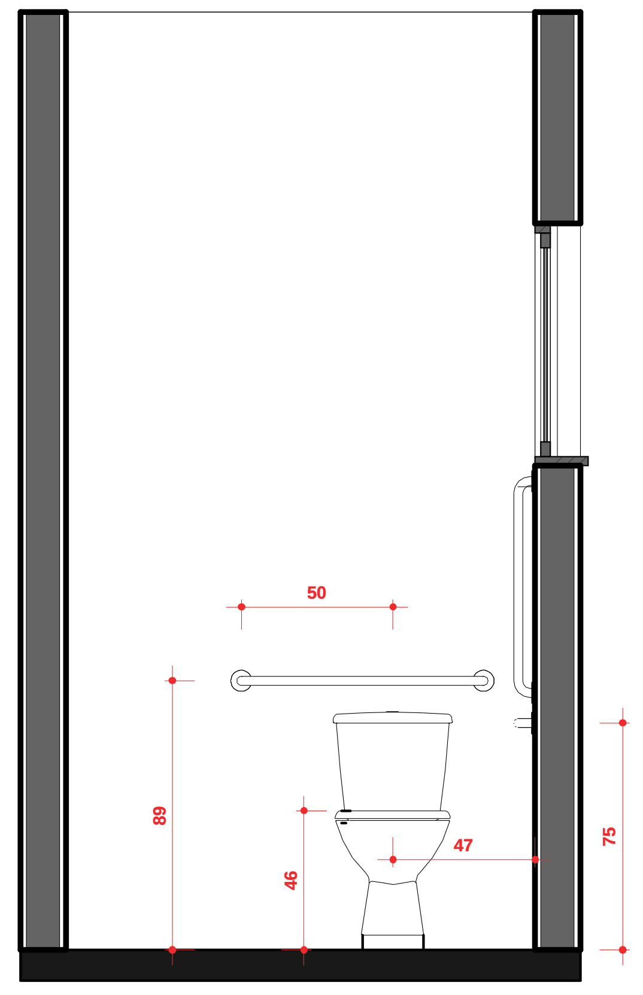

4 **CORTE BAN.05E06 - 1**

1 : 25

Nº	MODIFICAÇÕES / REVISÕES	RESP./PROJE	APROVADO	DATA
0	EMISSÃO INICIAL	ELIS	ELIS	21/04/2025
1	RETORNO	ELIS	ELIS	22/12/2025
2				
3				

ELIS REGINA
arquitetura & interiores

MICHEL HORN
engenharia & interiores

ACESSIBILIDADE

Obra: POUSADA VÔ TESTA
Área: **2.785,49**
Endereço: RODOVIA LAGO AZUL
Quadra: -
Lote:

PROPRIETÁRIO: FLÁVIO CALGARO

RESPONSÁVEL TÉCNICO: **ELIS REGINA STADTLOBER** ARQ. E URB. - CAU A116328-0

Conteúdo da folha:
ACESSIBILIDADE RECEPÇÃO
DETALHAMENTO BANHEIROS ACESSÍVEIS

Projetista: Autor
Escala: INDICADA
Data e Versão: 22/12/2025 - R01
Formato: **A1** - 841x594 mm

Prancha: **AC-05**

G:\Outros computadores\Meu laptop\Projetos Michel Horn\Clientes 2024\21-POUSADA VÔ TESTA\ACESSIBILIDADE\AC01-R01 POUSADA VÔ TESTA.rvt

OS DIREITOS AUTORAIS DESTE PROJETO SÃO RESERVADOS, É PROIBIDA SUA REPRODUÇÃO, MODIFICAÇÃO, ALTERAÇÃO E/OU SUA UTILIZAÇÃO INDEVIDA. LEI 5968 ART. 25.