
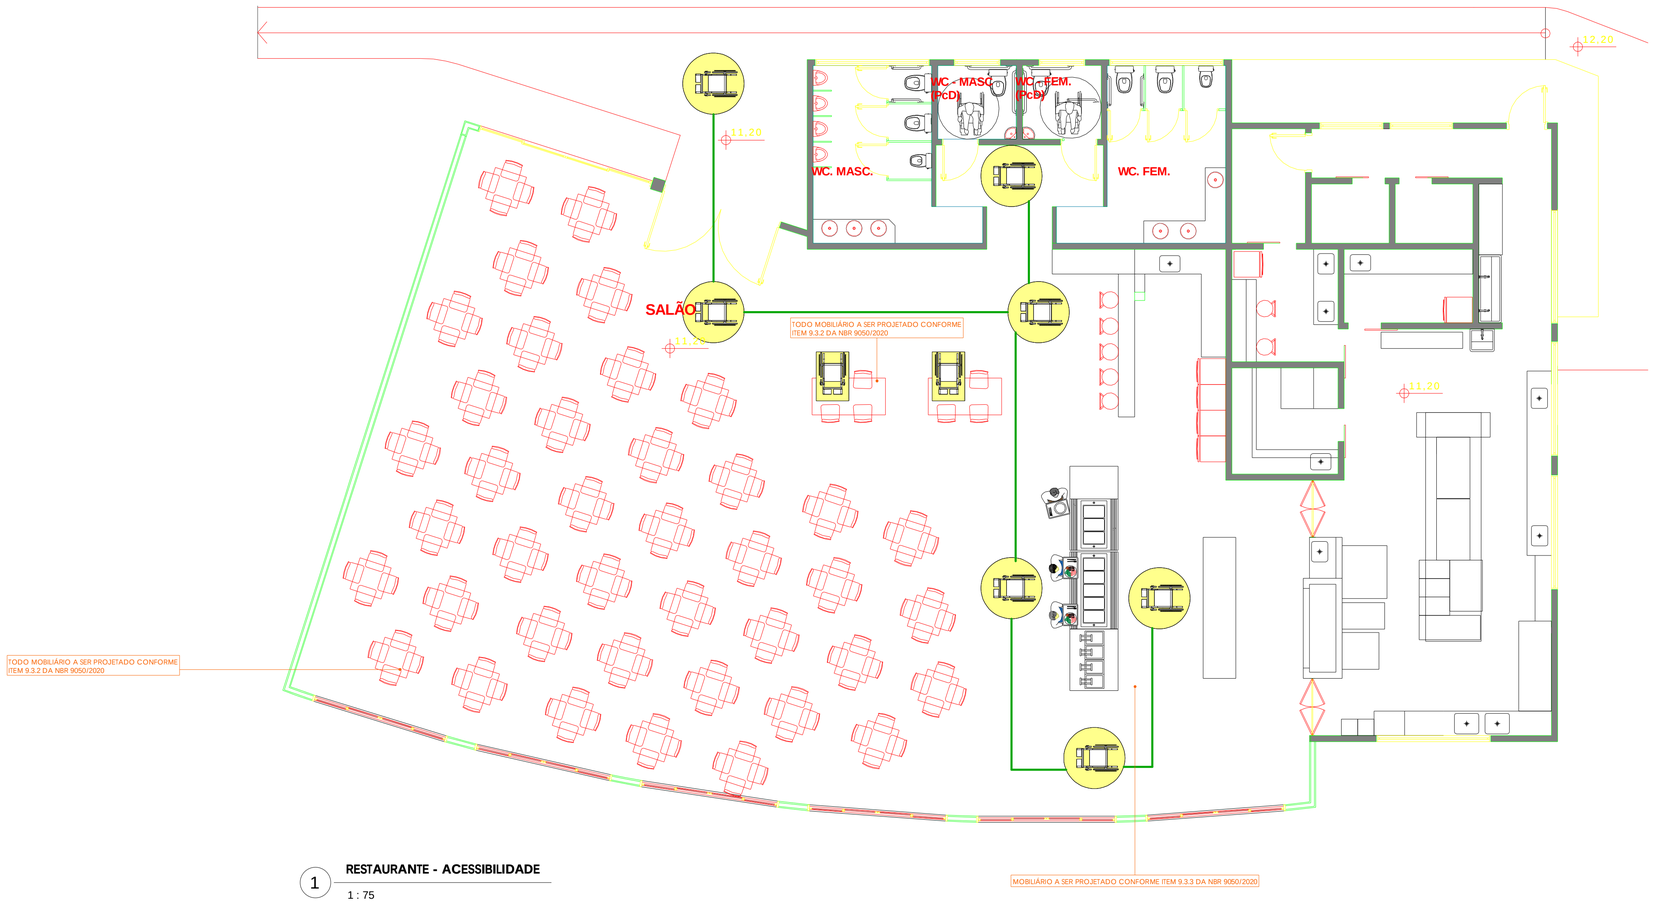



1 **RESTAURANTE - ACESSIBILIDADE**

1 : 75

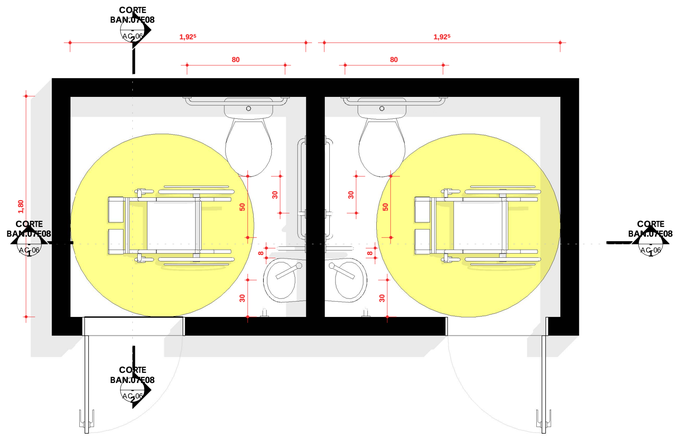


2 **DET. BANHEIRO 7 E 8**

1 : 25

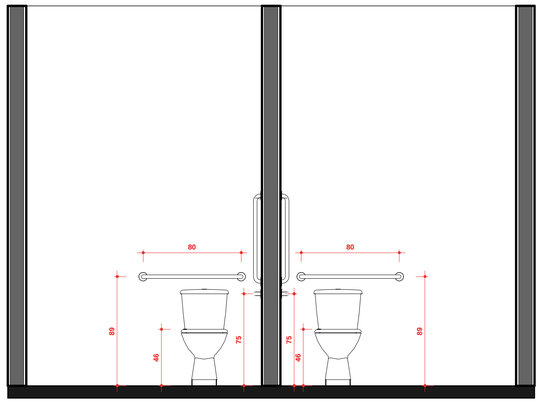

3 **CORTE BAN.07E08 - 1**

1 : 25

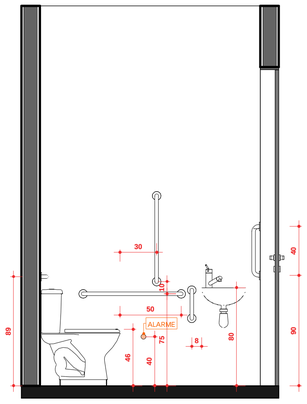

4 **CORTE BAN.07E08 - 2**

1 : 25

HAVERÁ FUNCIONÁRIOS PARA A COMUNICAÇÃO COM PESSOAS COM DEFICIÊNCIA, PRINCIPALMENTE NO QUE DIZ RESPEITO AOS SERVIÇOS DE RESTAURANTE;
SALAS DE REFEIÇÕES DEVEM DISPOR DE NO MÍNIMO UM EXEMPLAR ATUALIZADO, IMPRESSO EM BRAILLE E EM TIPOLOGIA AMPLIADA;

Nº	MODIFICAÇÕES / REVISÕES	RESP./PROJE	APROVADO	DATA
0	EMISSÃO INICIAL	ELIS	ELIS	21/04/2025
1	RETORNO	ELIS	ELIS	22/12/2025
2				
3				

ELIS REGINA arquitetura & interiores

MICHEL HORN engenharia & interiores

ACESSIBILIDADE

Obra: POUSADA VÔ TESTA

Área: 2.785,49

Endereço: RODOVIA LAGO AZUL

Quadra: -

Lote:

PROPRIETÁRIO: FLÁVIO CALGARO

RESPONSÁVEL TÉCNICO: **ELIS REGINA STADTLOBER** ARQ. E URB. - CAU A116328-0

Conteúdo da folha: RESTAURANTE ACESSIBILIDADE
DETALHAMENTO BANHEIROS ACESSÍVEIS

Projetista: Autor

Escala: INDICADA

Data e Versão: 22/12/2025 - R01

Formato: **A1** - 841x594 mm

Prancha: **AC-06**

© Direitos computadorizados Mac/Laptop/Projetos Michel Horn/Cheres 2024/23-POUSADA VÔ TESTA/ACESSIBILIDADE/ACS 06 01 POUSADA VÔ TESTA .vt

OS DIREITOS AUTORAIS DESTE PROJETO SÃO RESERVADOS, É PROIBIDA SUA REPRODUÇÃO, MODIFICAÇÃO, ALTERAÇÃO E/OU SUA UTILIZAÇÃO INDEVIDA, LEI 5968 ART. 25.