
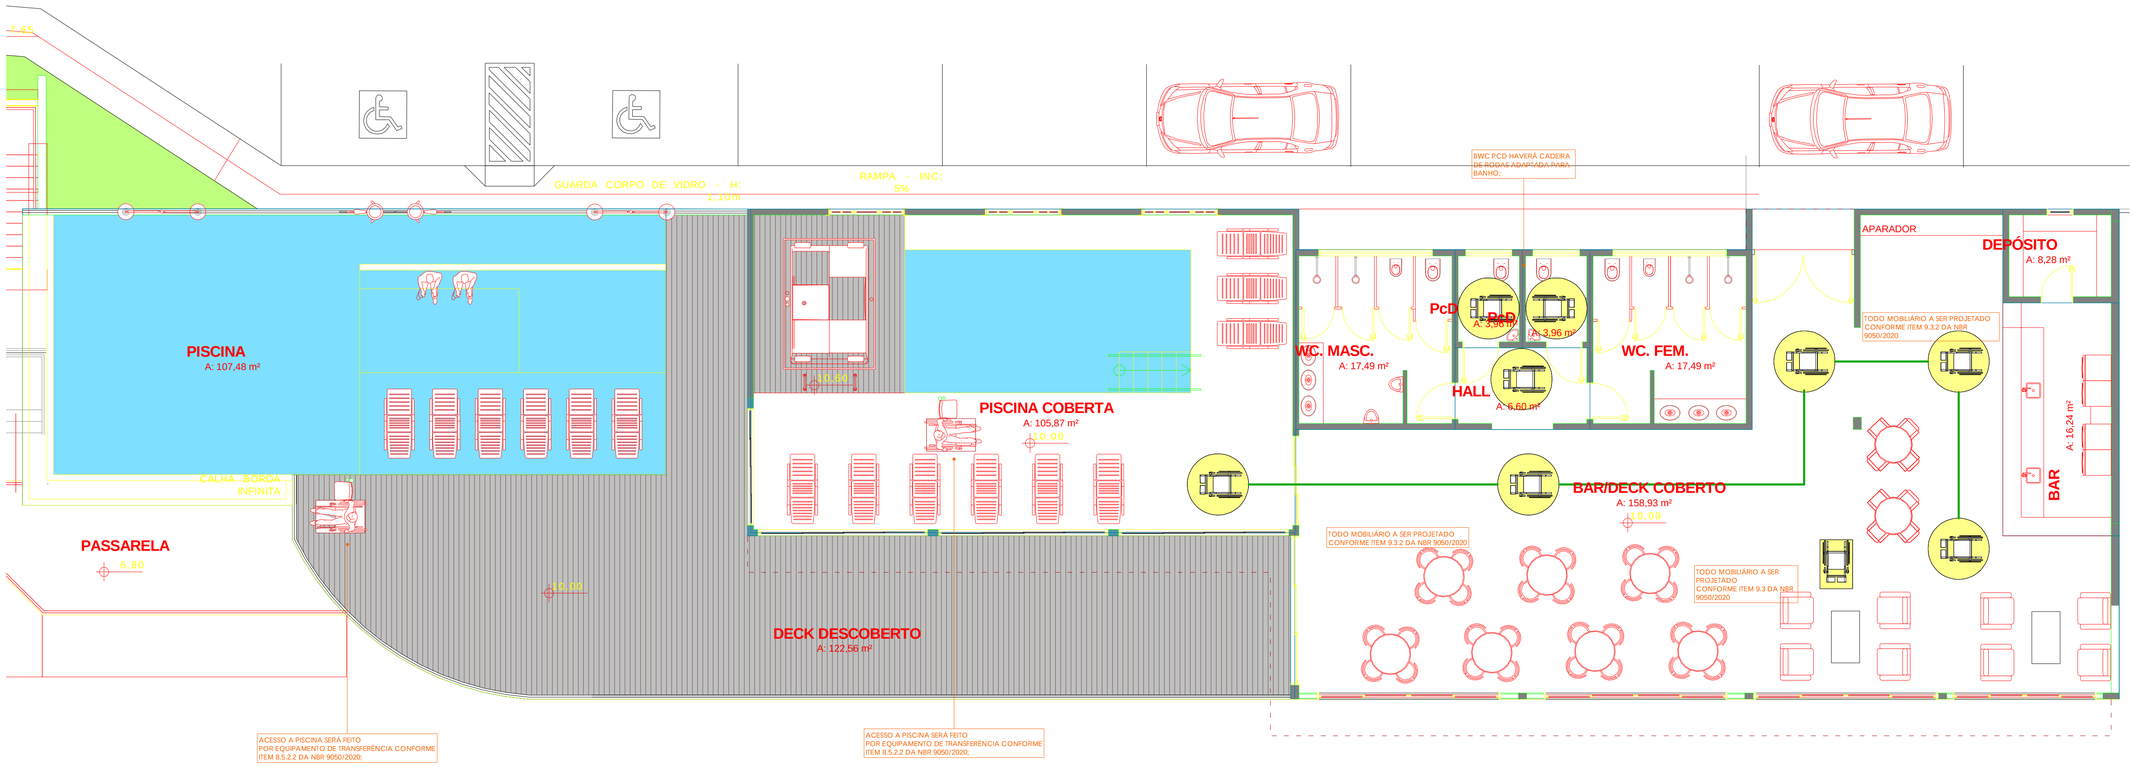



1 **PISCINA - ACESSIBILIDADE**

1 : 75

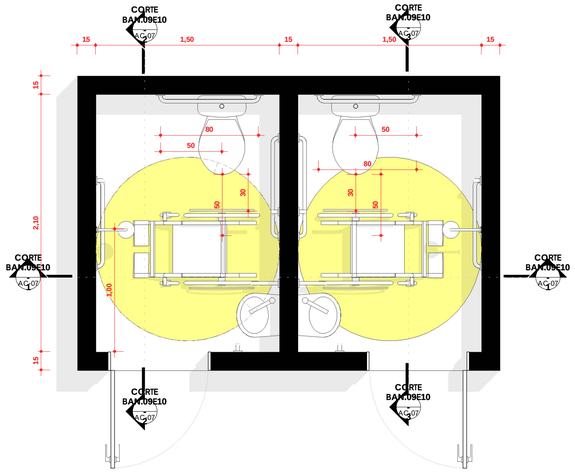


2 **DET. BANHEIRO 7 E 8**

1 : 25

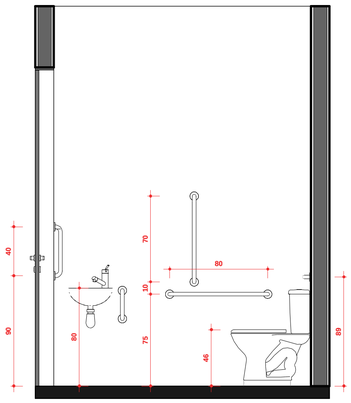


3 **CORTE BAN.09E10 - 3**

1 : 25

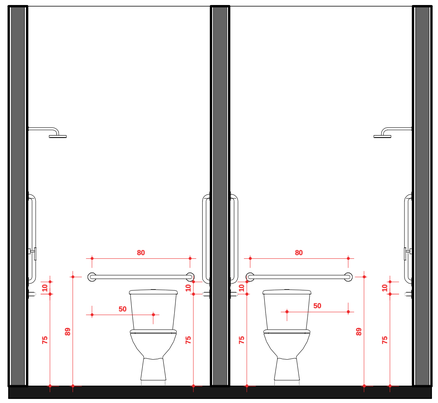


4 **CORTE BAN.09E10 - 1**

1 : 25

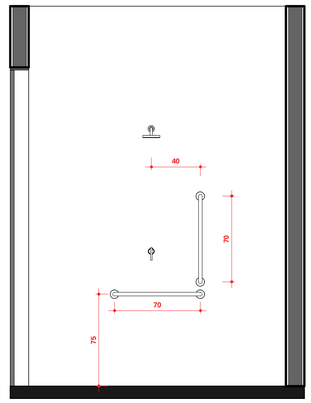


5 **CORTE BAN.09E10 - 2**

1 : 25

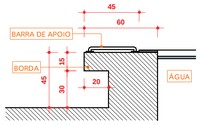


7 **CORTE JACUZZI**

1 : 25

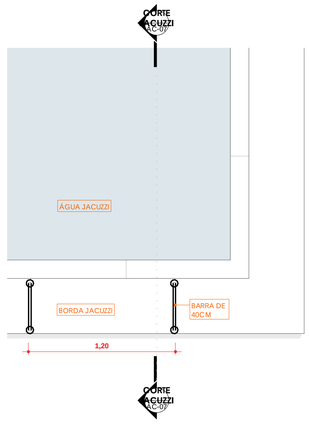


6 **PLANTA JACUZZI**

1 : 25

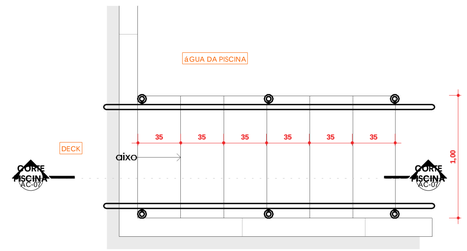

8 **PLANTA PISCINA**

1 : 25

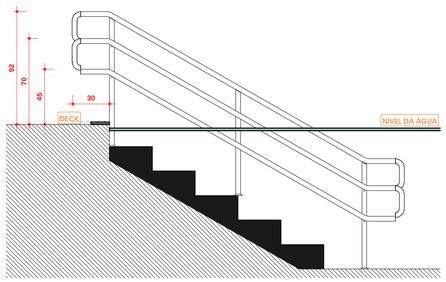

9 **CORTE PISCINA**

1 : 25

Nº	MODIFICAÇÕES / REVISÕES	RESP./PROJE	APROVADO	DATA
0	EMISSÃO INICIAL	ELIS	ELIS	21/04/2025
1	RETORNO	ELIS	ELIS	22/12/2025
2				
3				

ELIS REGINA arquitetura & interiores

MICHEL HORN engenharia & interiores

ACESSIBILIDADE

Obra: POUSADA VÔ TESTA

Área: 2.785,49

Endereço: RODOVIA LAGO AZUL

Quadra: -

Lote:

PROPRIETÁRIO: FLÁVIO CALGARO

RESPONSÁVEL TÉCNICO: **ELIS REGINA STADTLOBER** ARQ. E URB. - CAU A116328-0

Conteúdo da folha: PISCINA ACESSIBILIDADE
DETALHAMENTO BANHEIROS ACESSÍVEIS

Projetista: Autor

Escala: INDICADA

Data e Versão: 22/12/2025 - R01

Formato: **A1** - 841x594 mm

Prancha: **AC-07**

OS DIREITOS AUTORAIS DESTE PROJETO SÃO RESERVADOS, É PROIBIDA SUA REPRODUÇÃO, MODIFICAÇÃO, ALTERAÇÃO E/OU SUA UTILIZAÇÃO INDEVIDA. LEI 5968 ART. 25.